
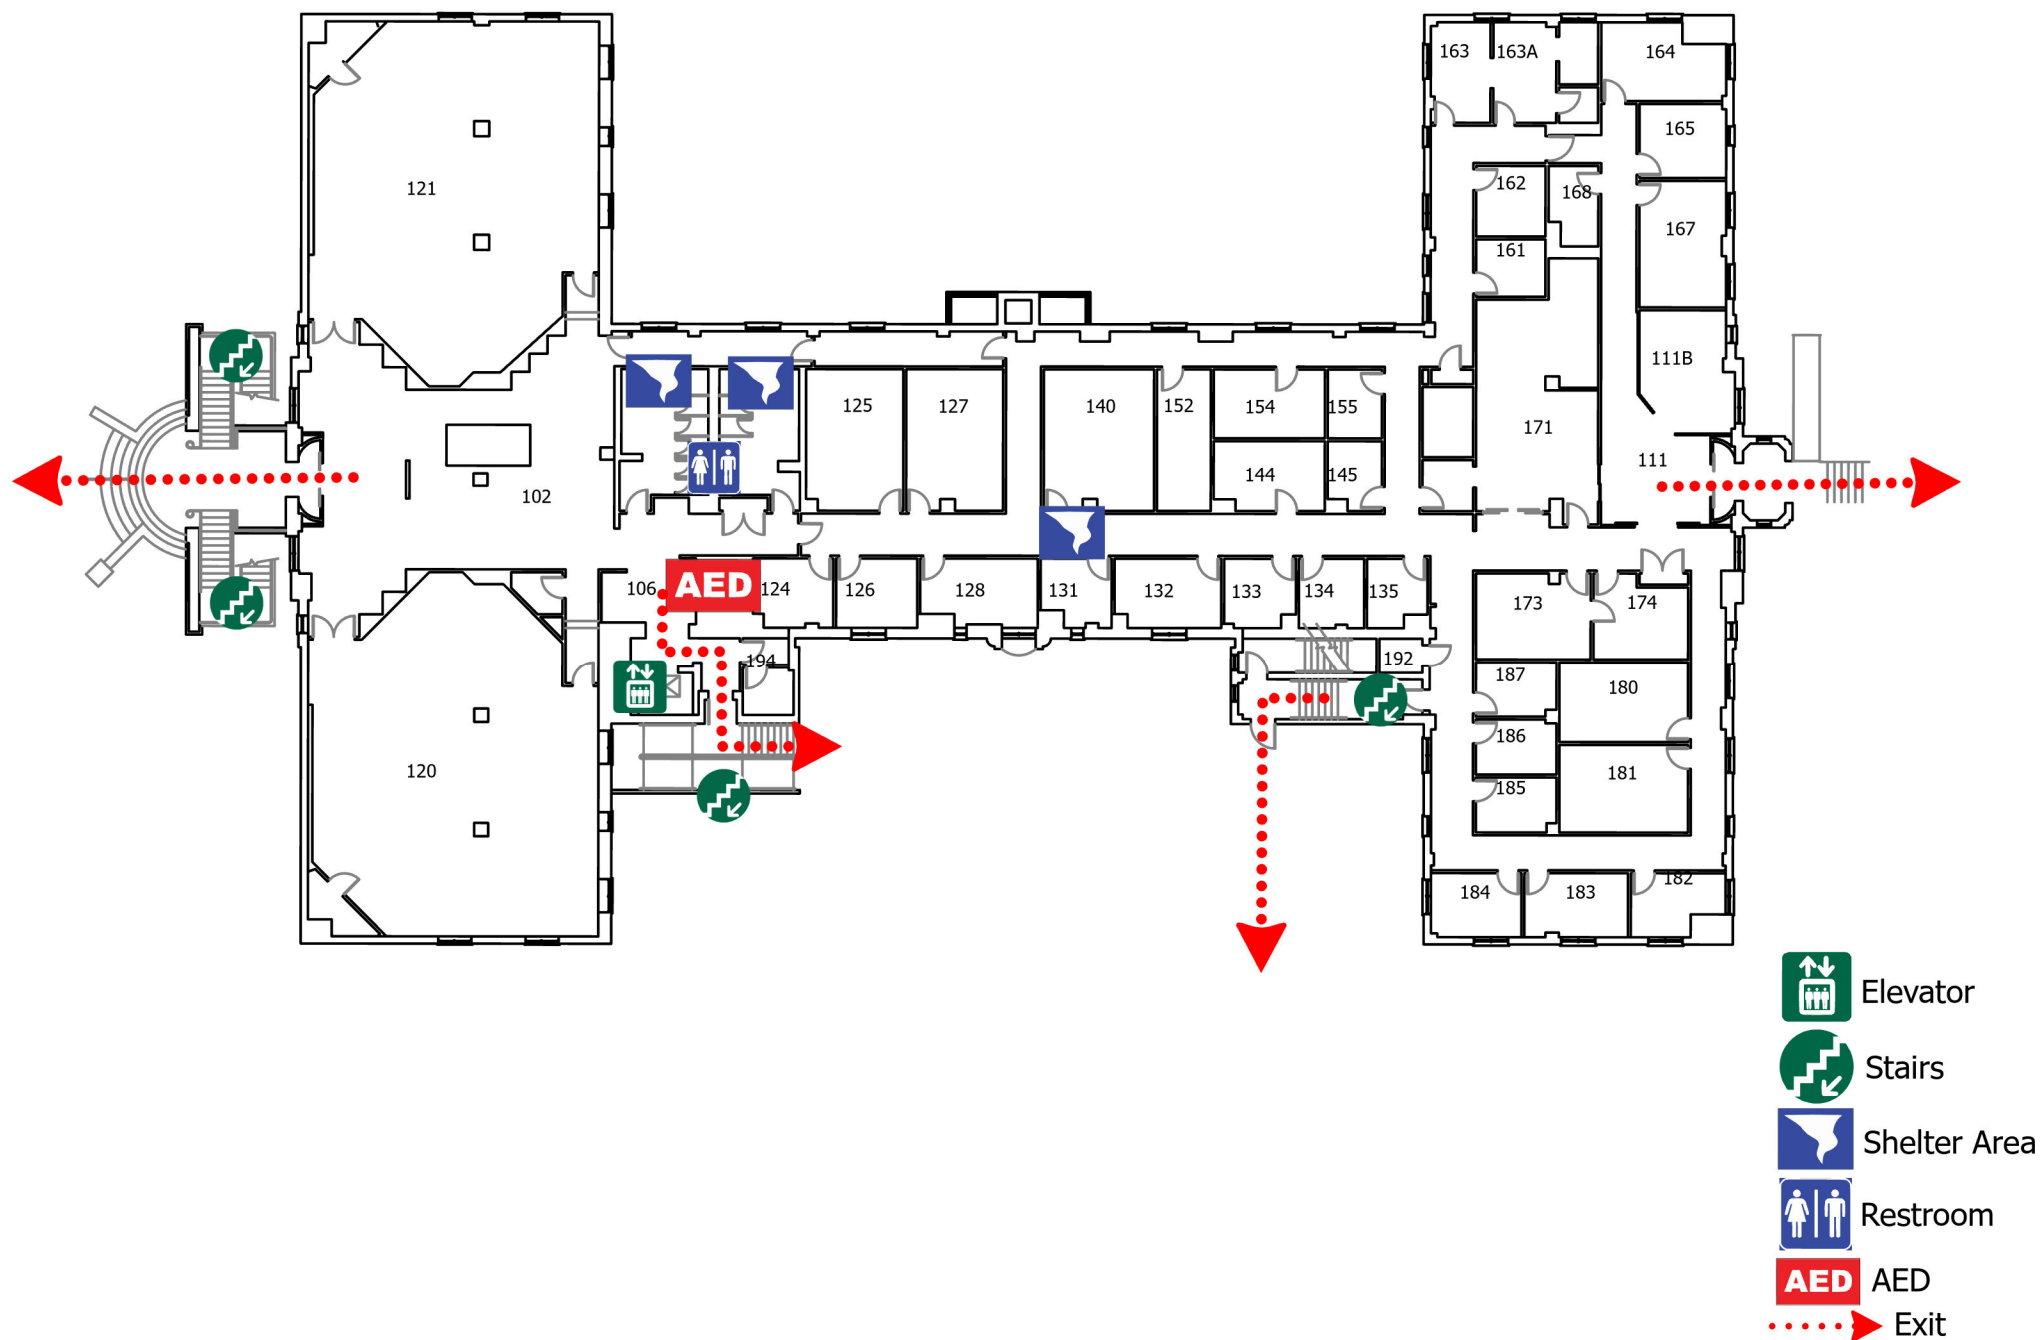


$\triangleright Z$ 

TERRILL HALL

SECOND FLOOR

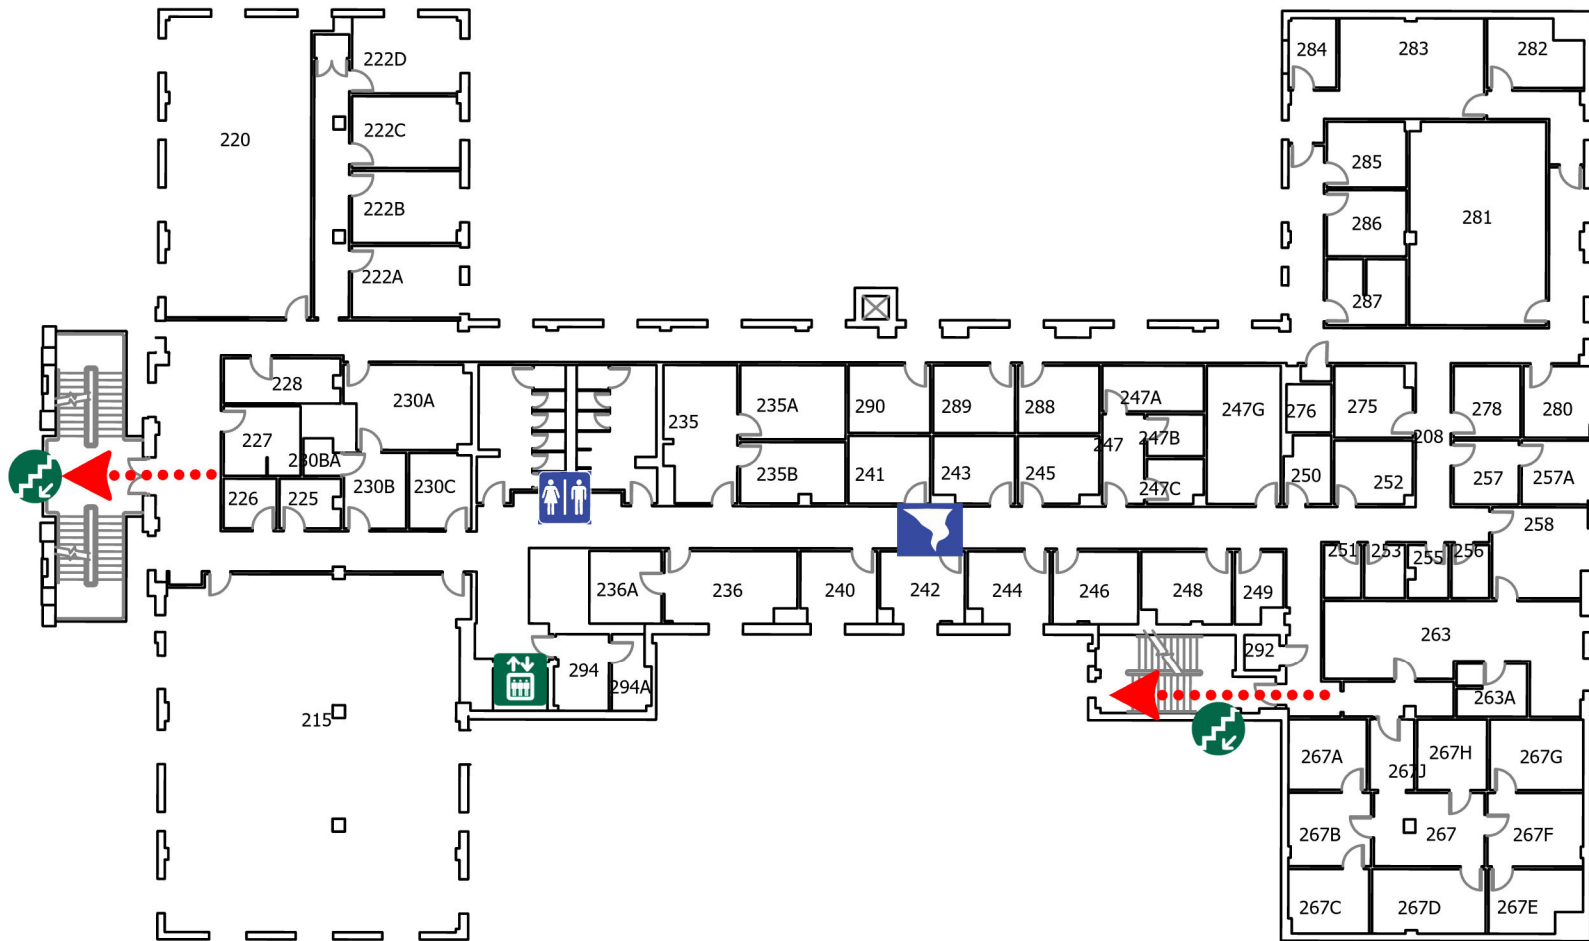

TERRILL HALL

THIRD FLOOR

