


# RAWLINS HALL


## FIRST FLOOR

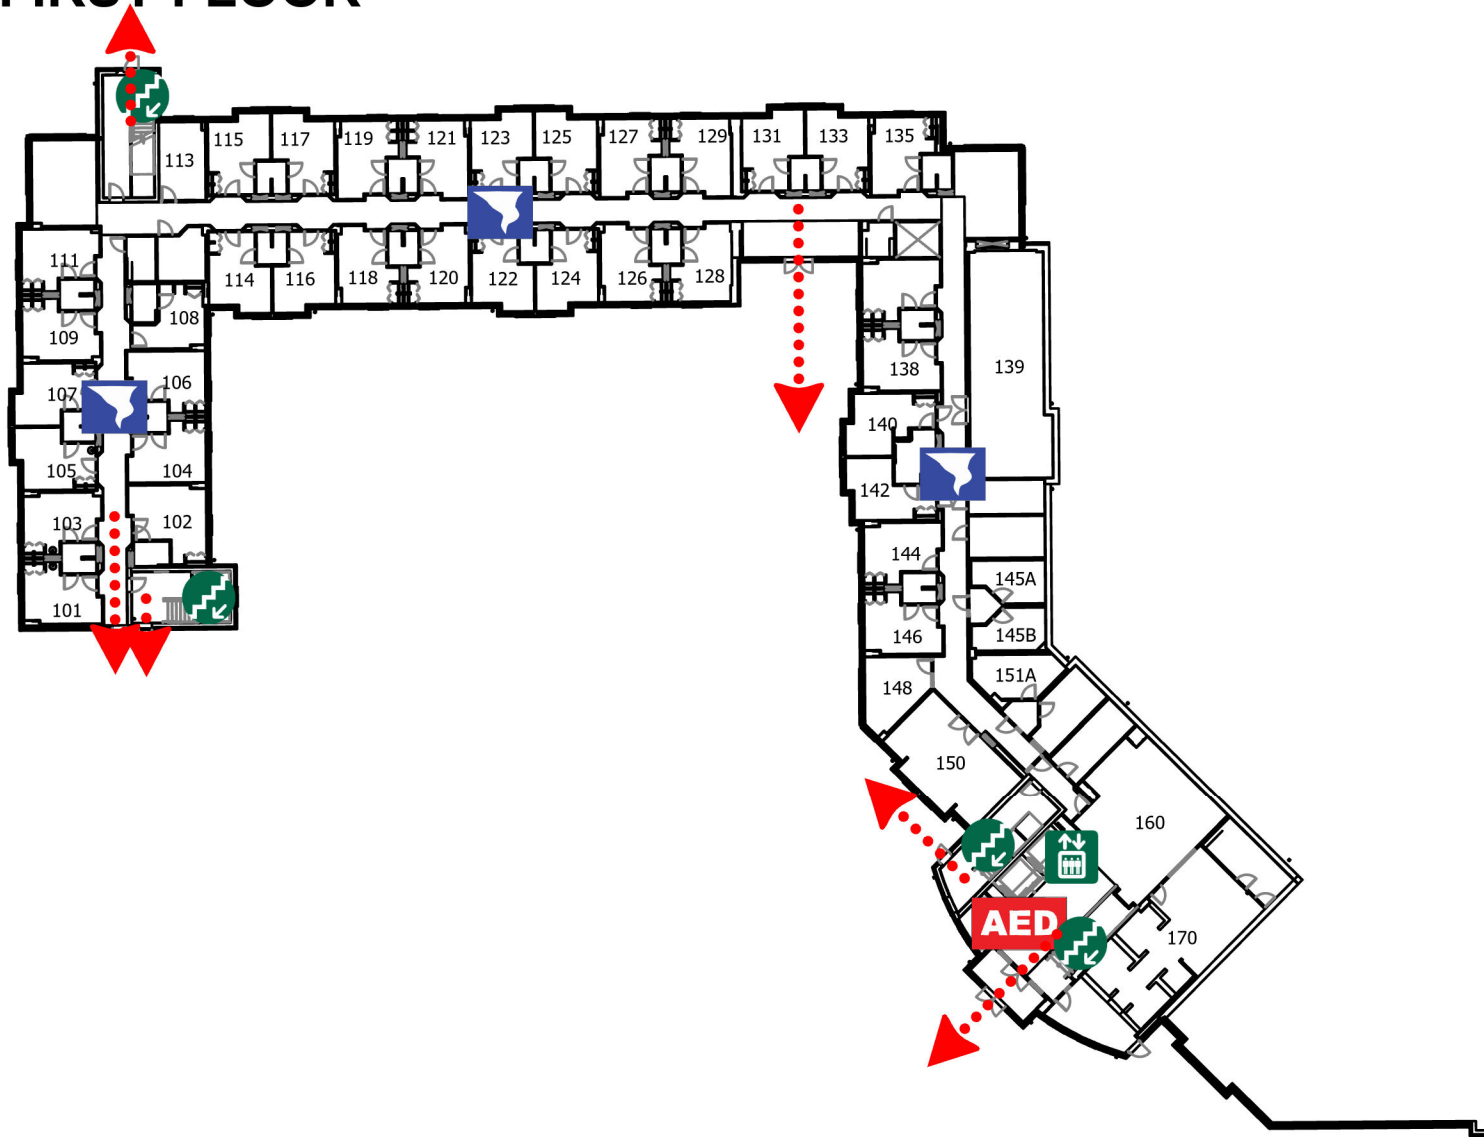

-  Elevator
-  Stairs
-  Shelter Area
-  AED
-  Exit


# RAWLINS HALL

## SECOND FLOOR

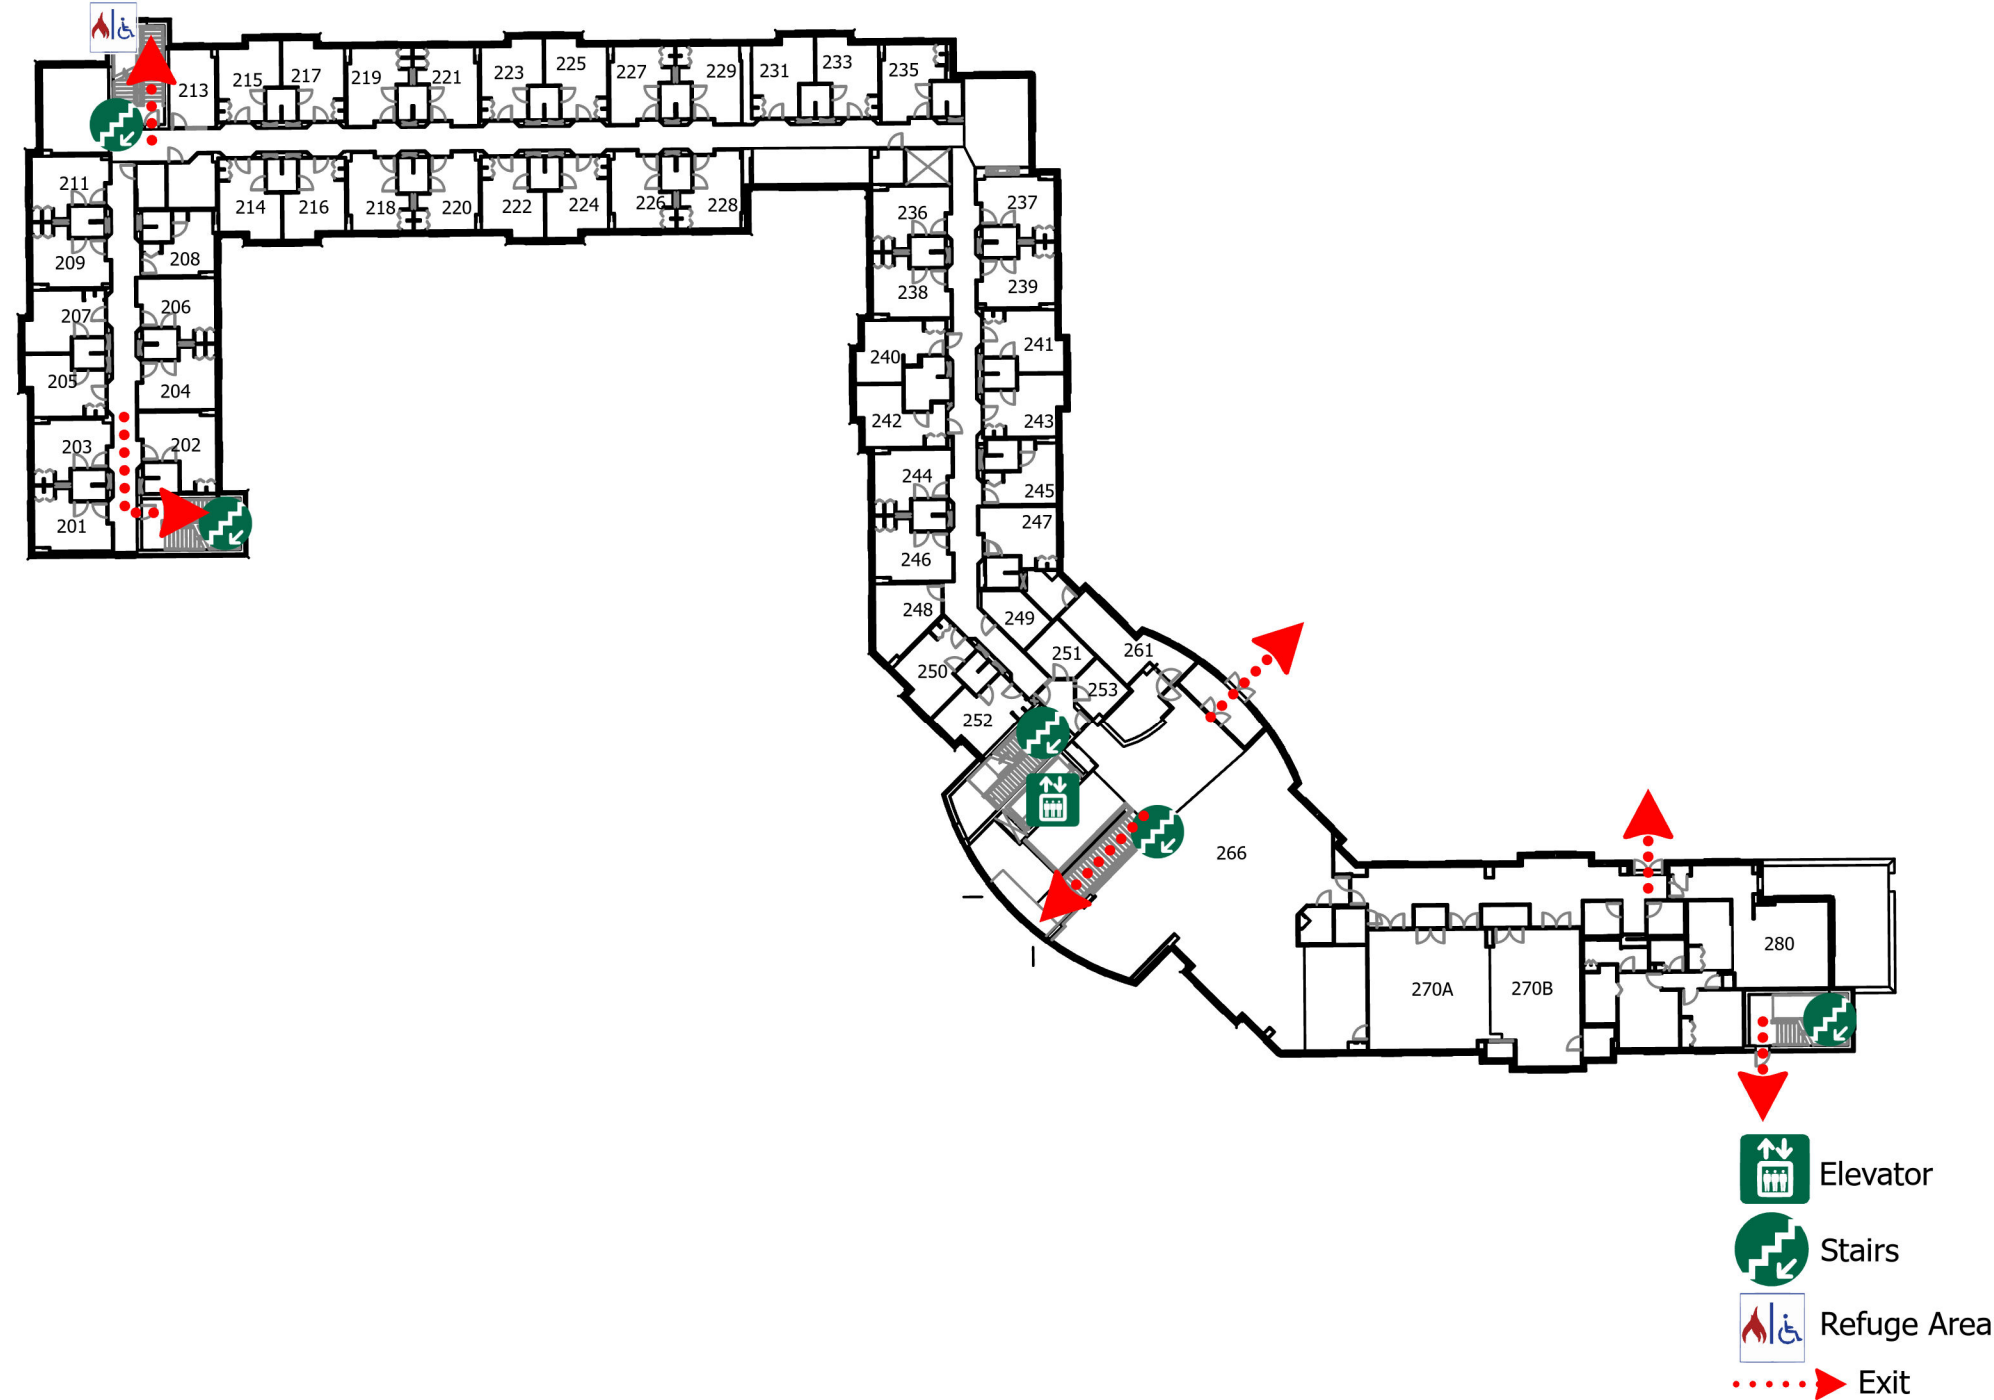

# RAWLINS HALL


## THIRD FLOOR

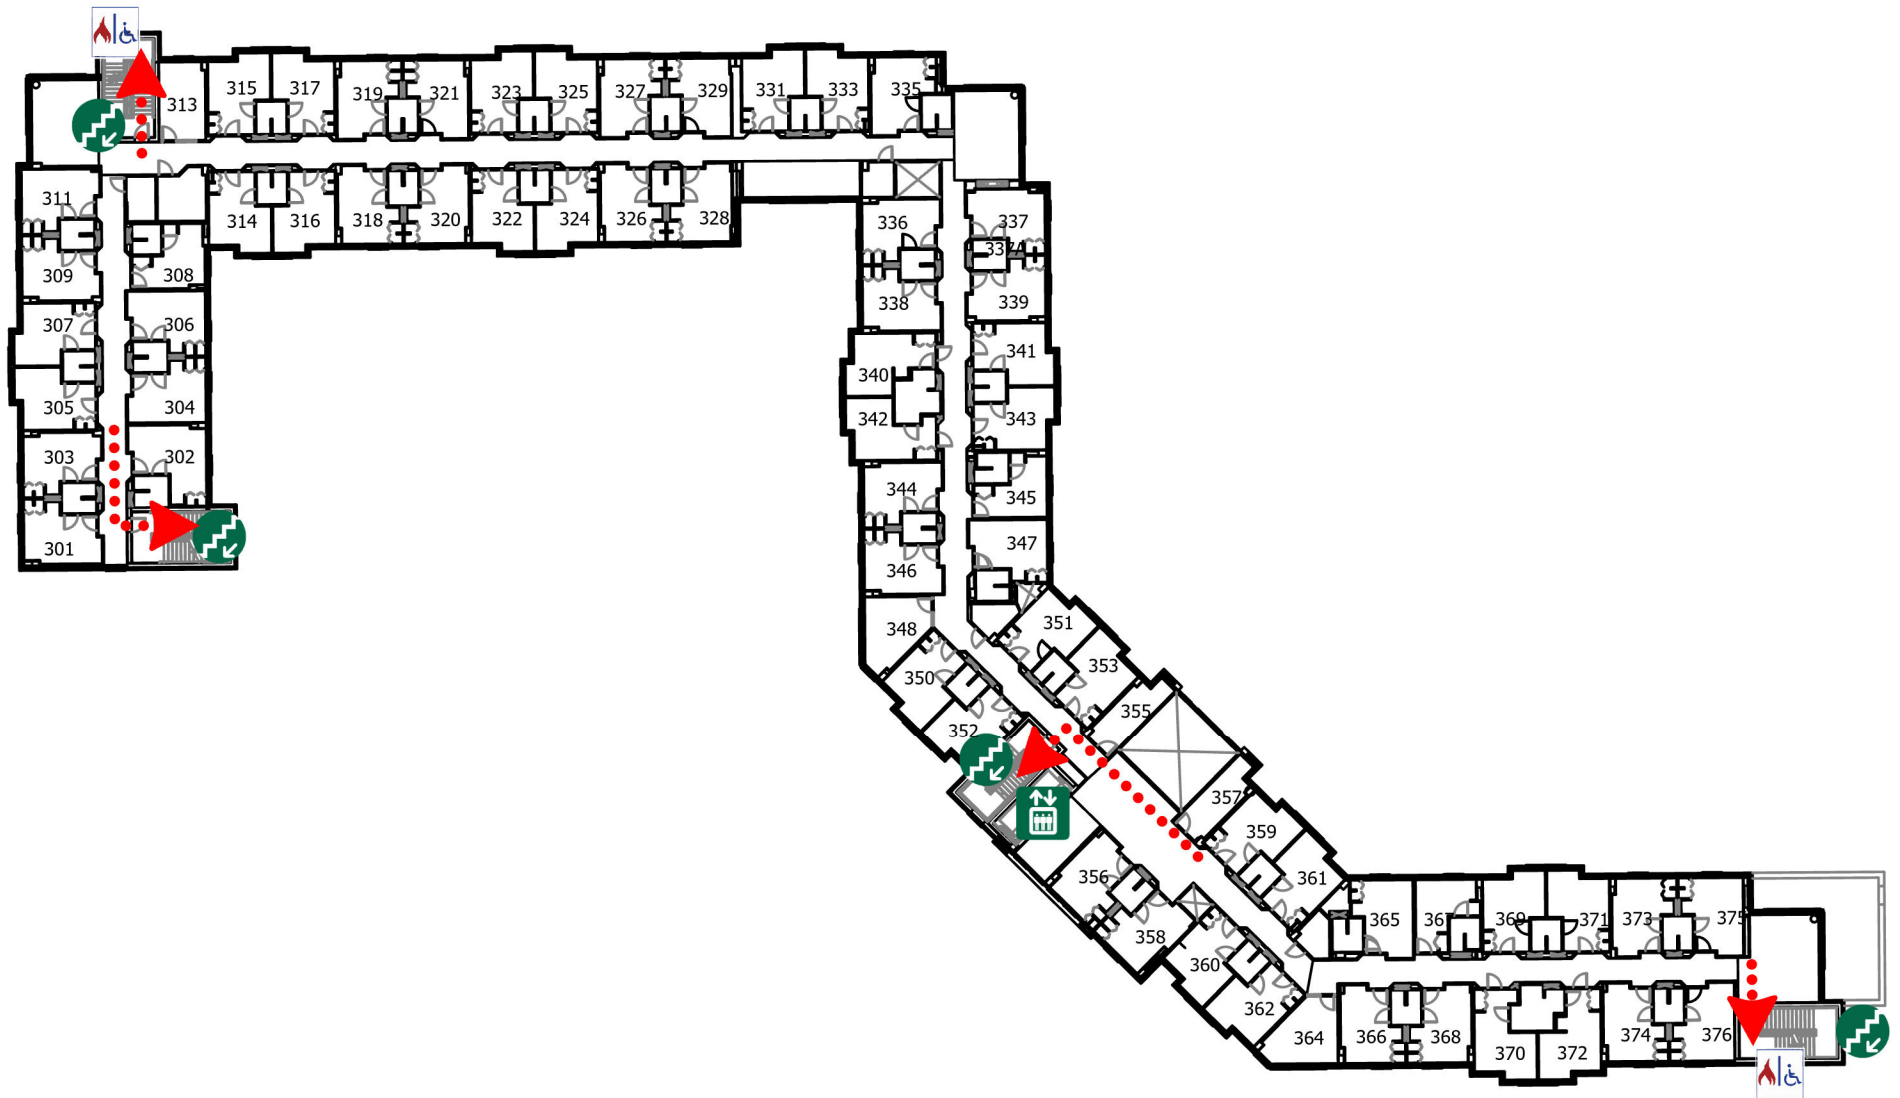

-  Elevator
-  Stairs
-  Refuge Area
-  Exit


# RAWLINS HALL

## FOURTH FLOOR

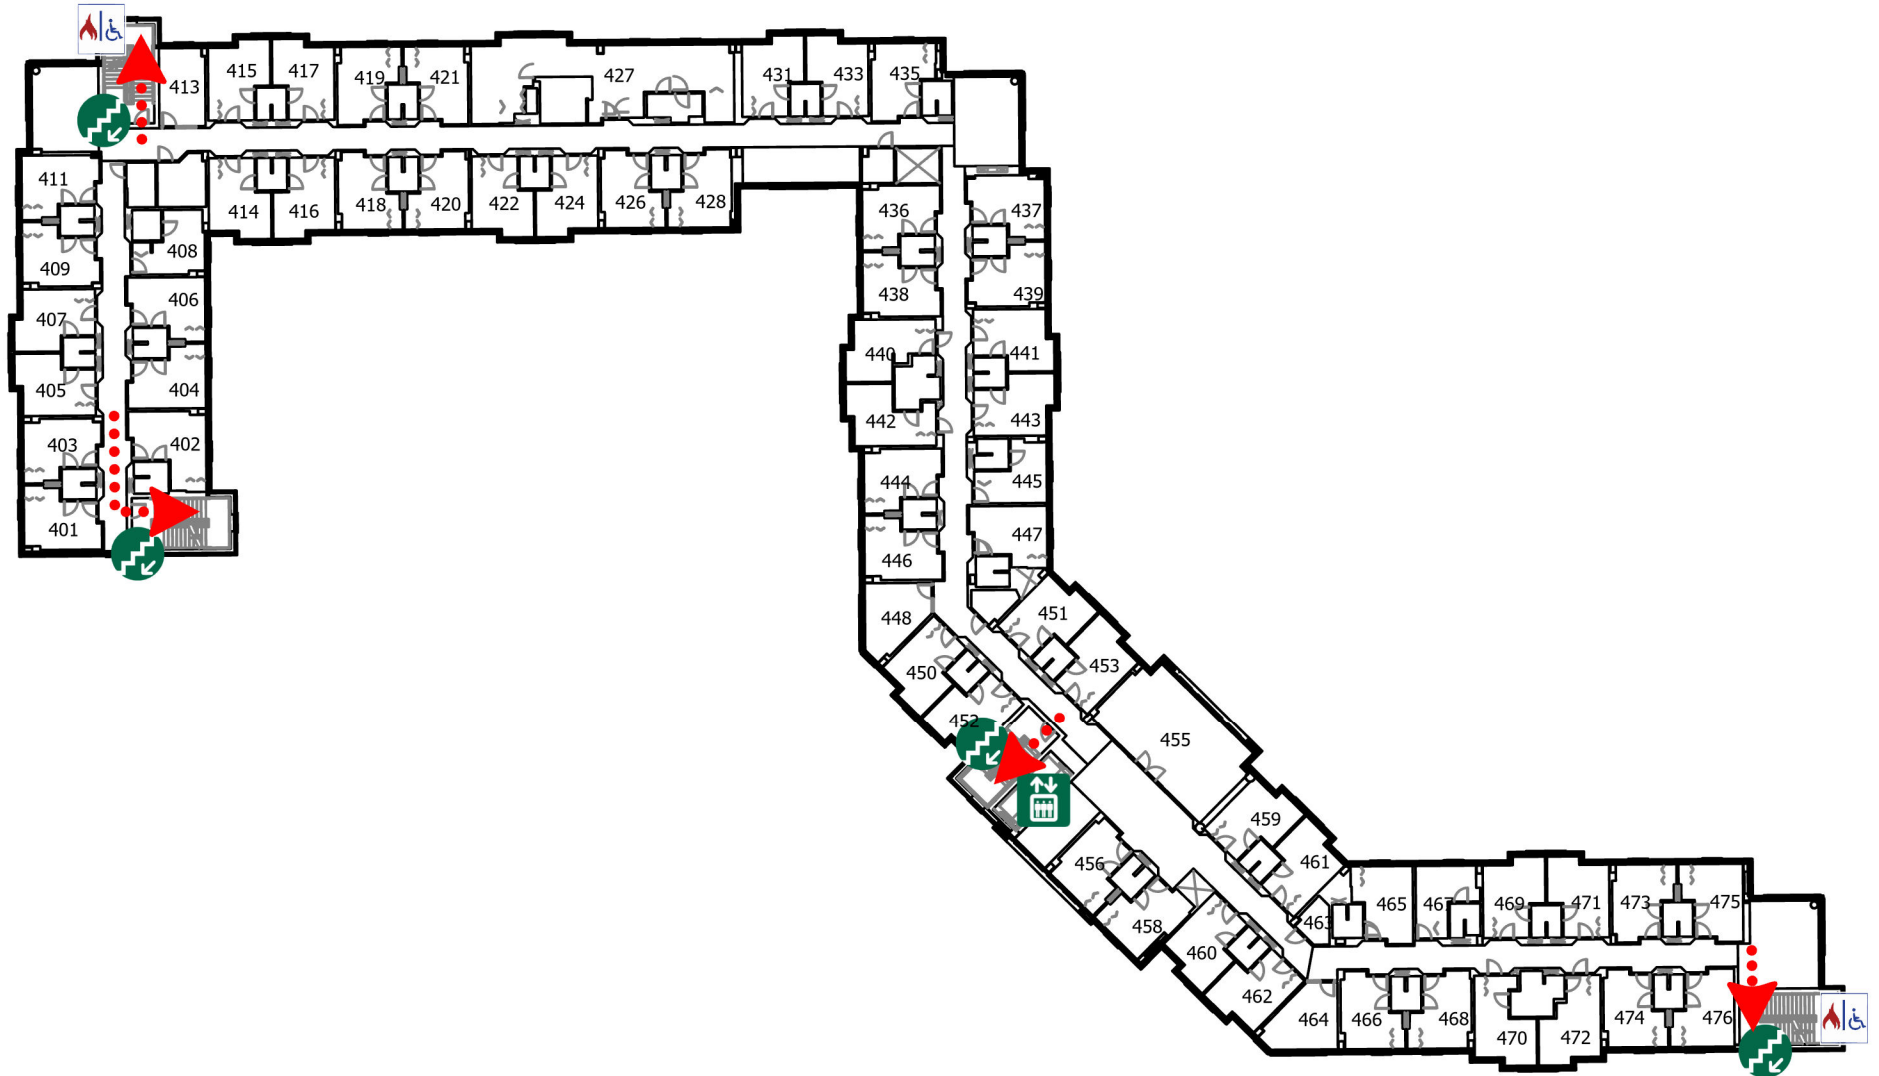

-  Elevator
-  Stairs
-  Refuge Area
-  Exit

# RAWLINS HALL FIFTH FLOOR

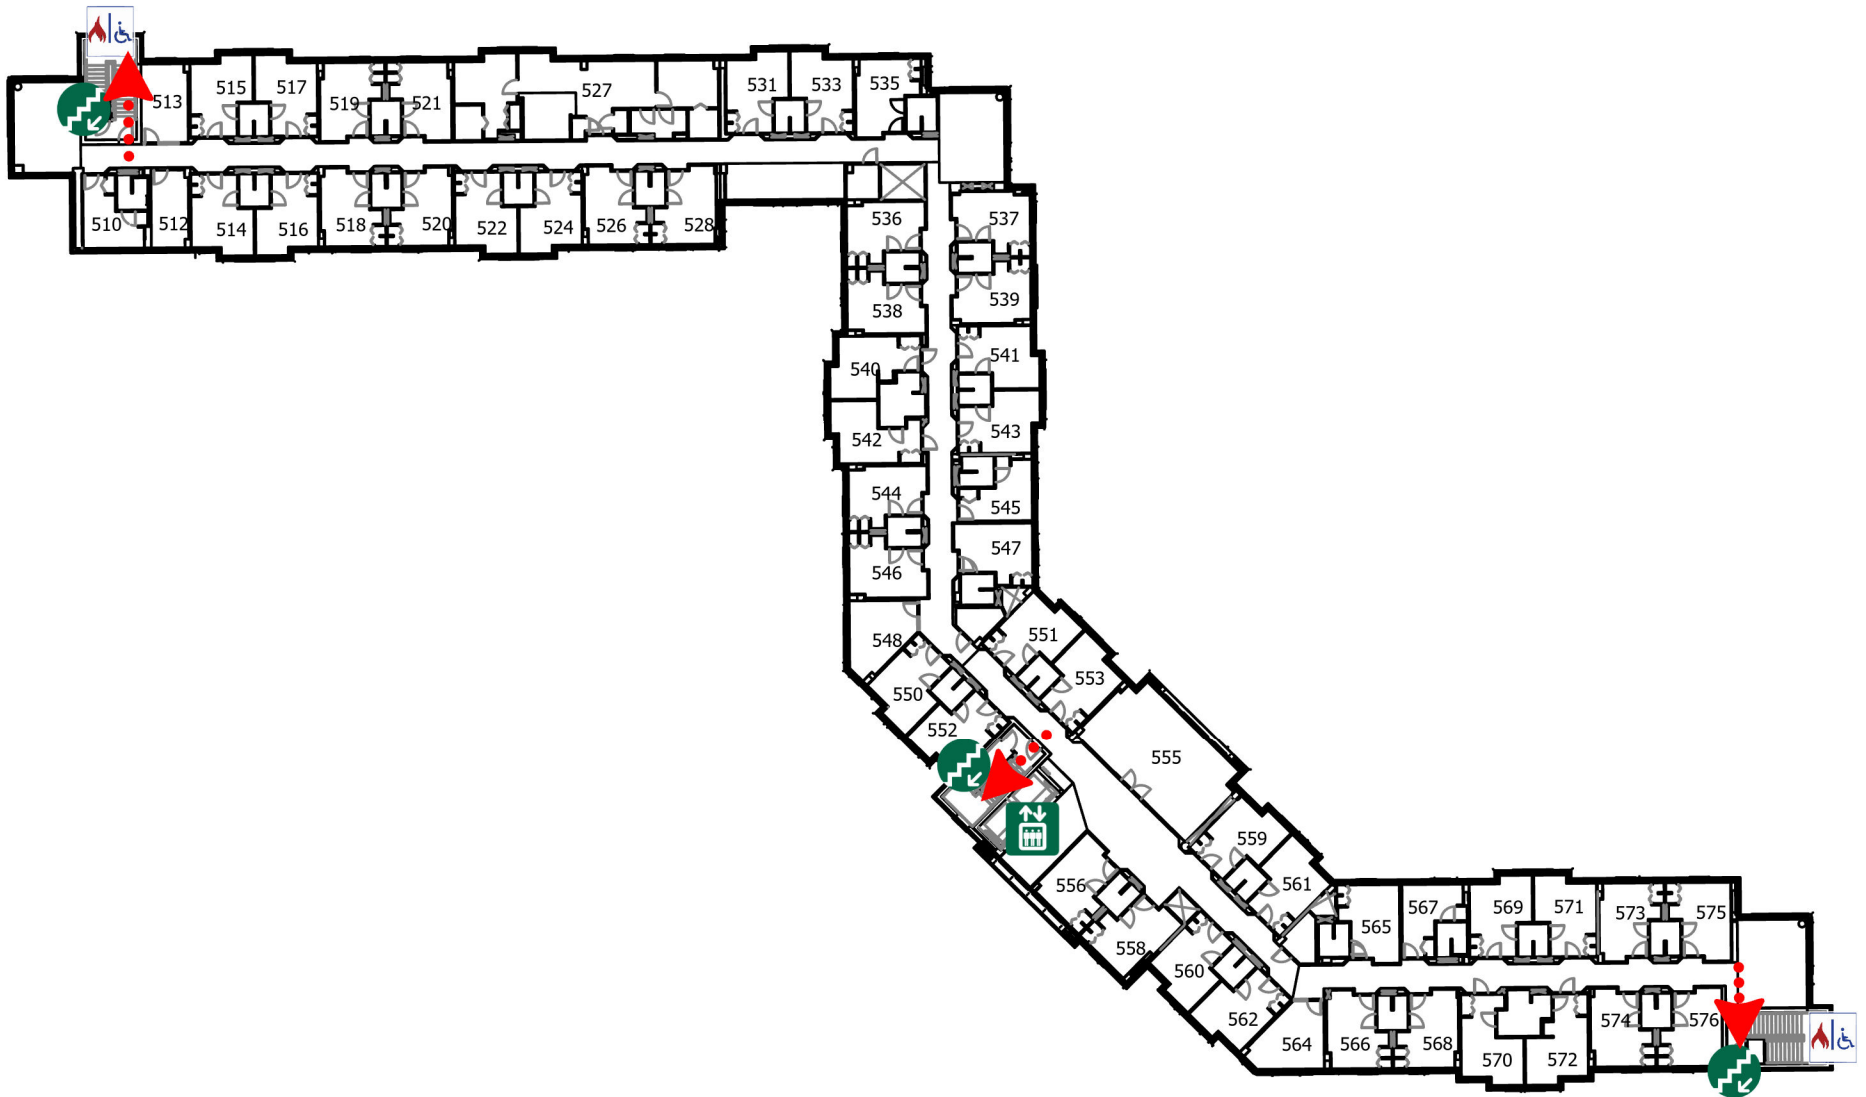

-  Elevator
-  Stairs
-  Refuge Area
-  Exit