


# CRUMLEY HALL

## FIRST FLOOR

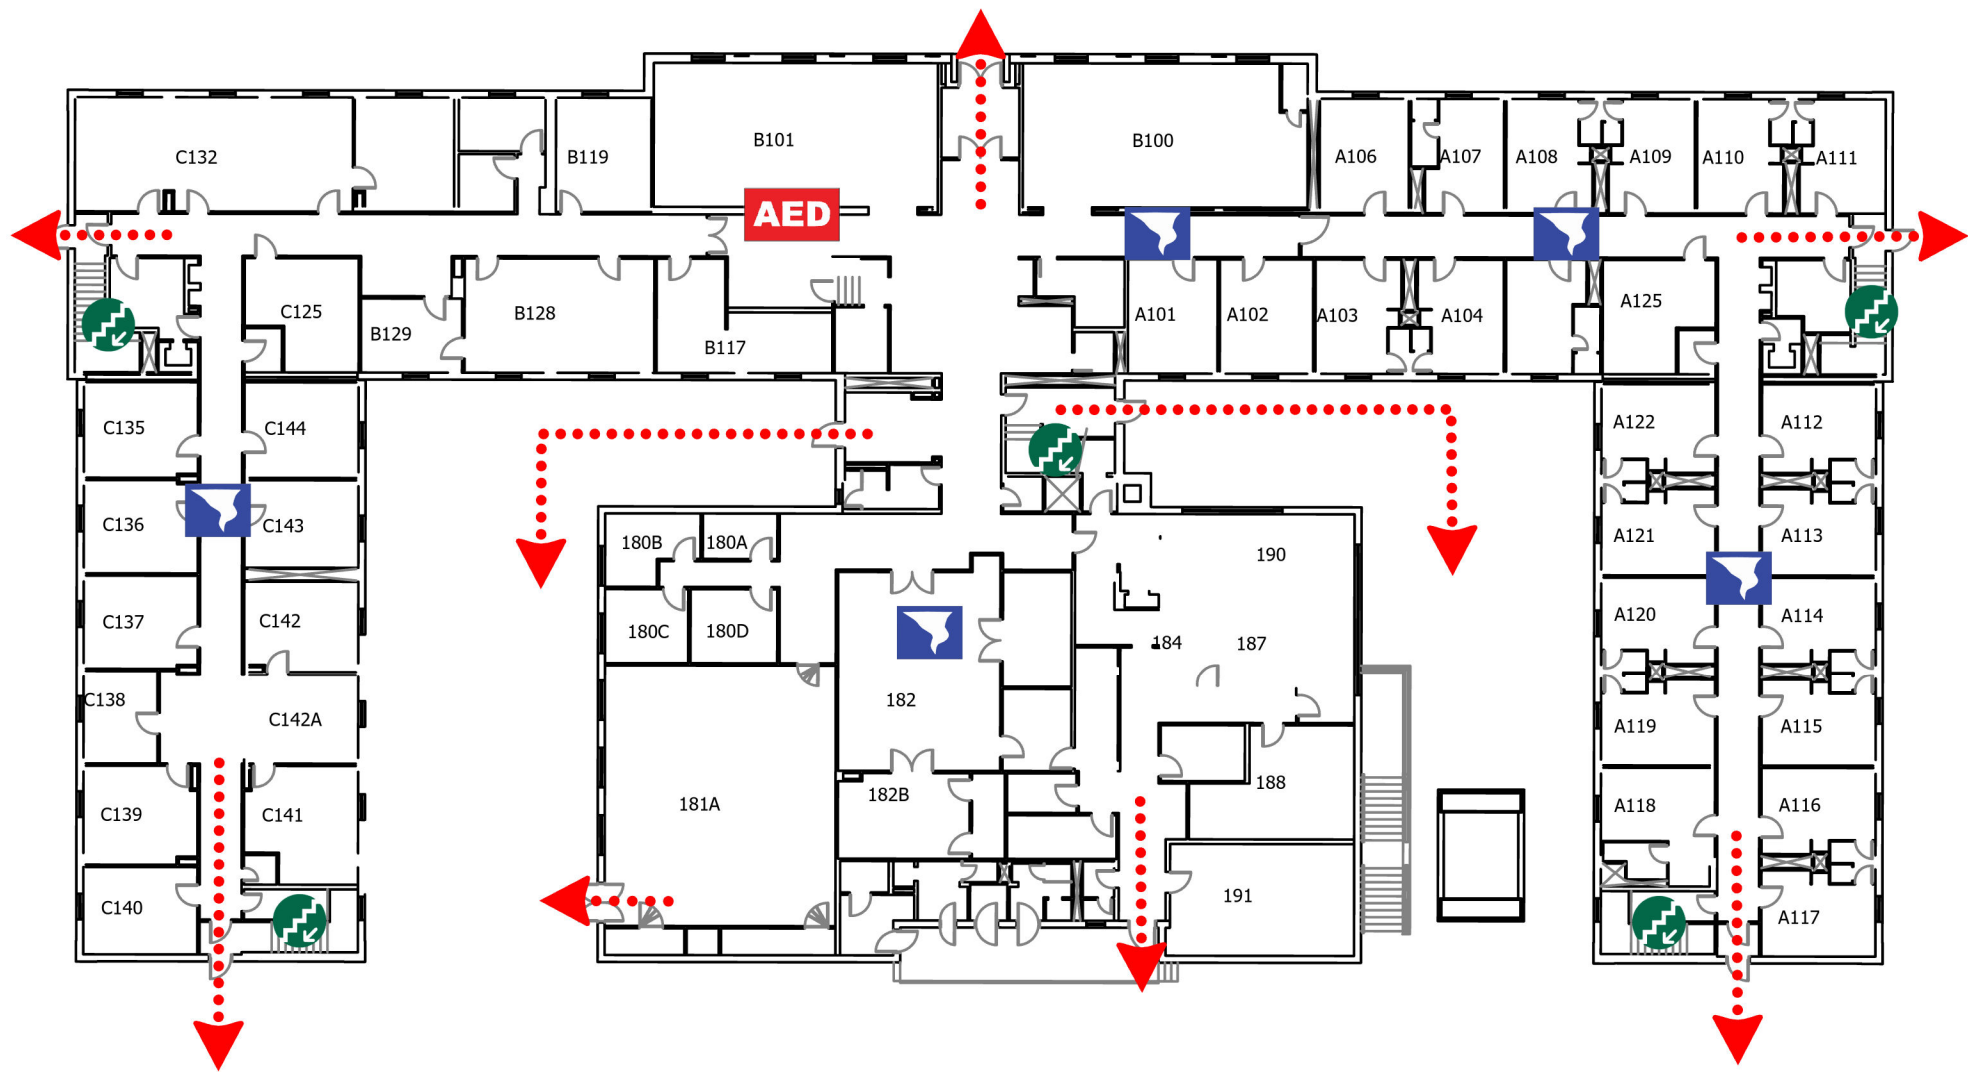

Stairs



Shelter Area



AED




Exit

# CRUMLEY HALL SECOND FLOOR



# CRUMLEY HALL

## THIRD FLOOR

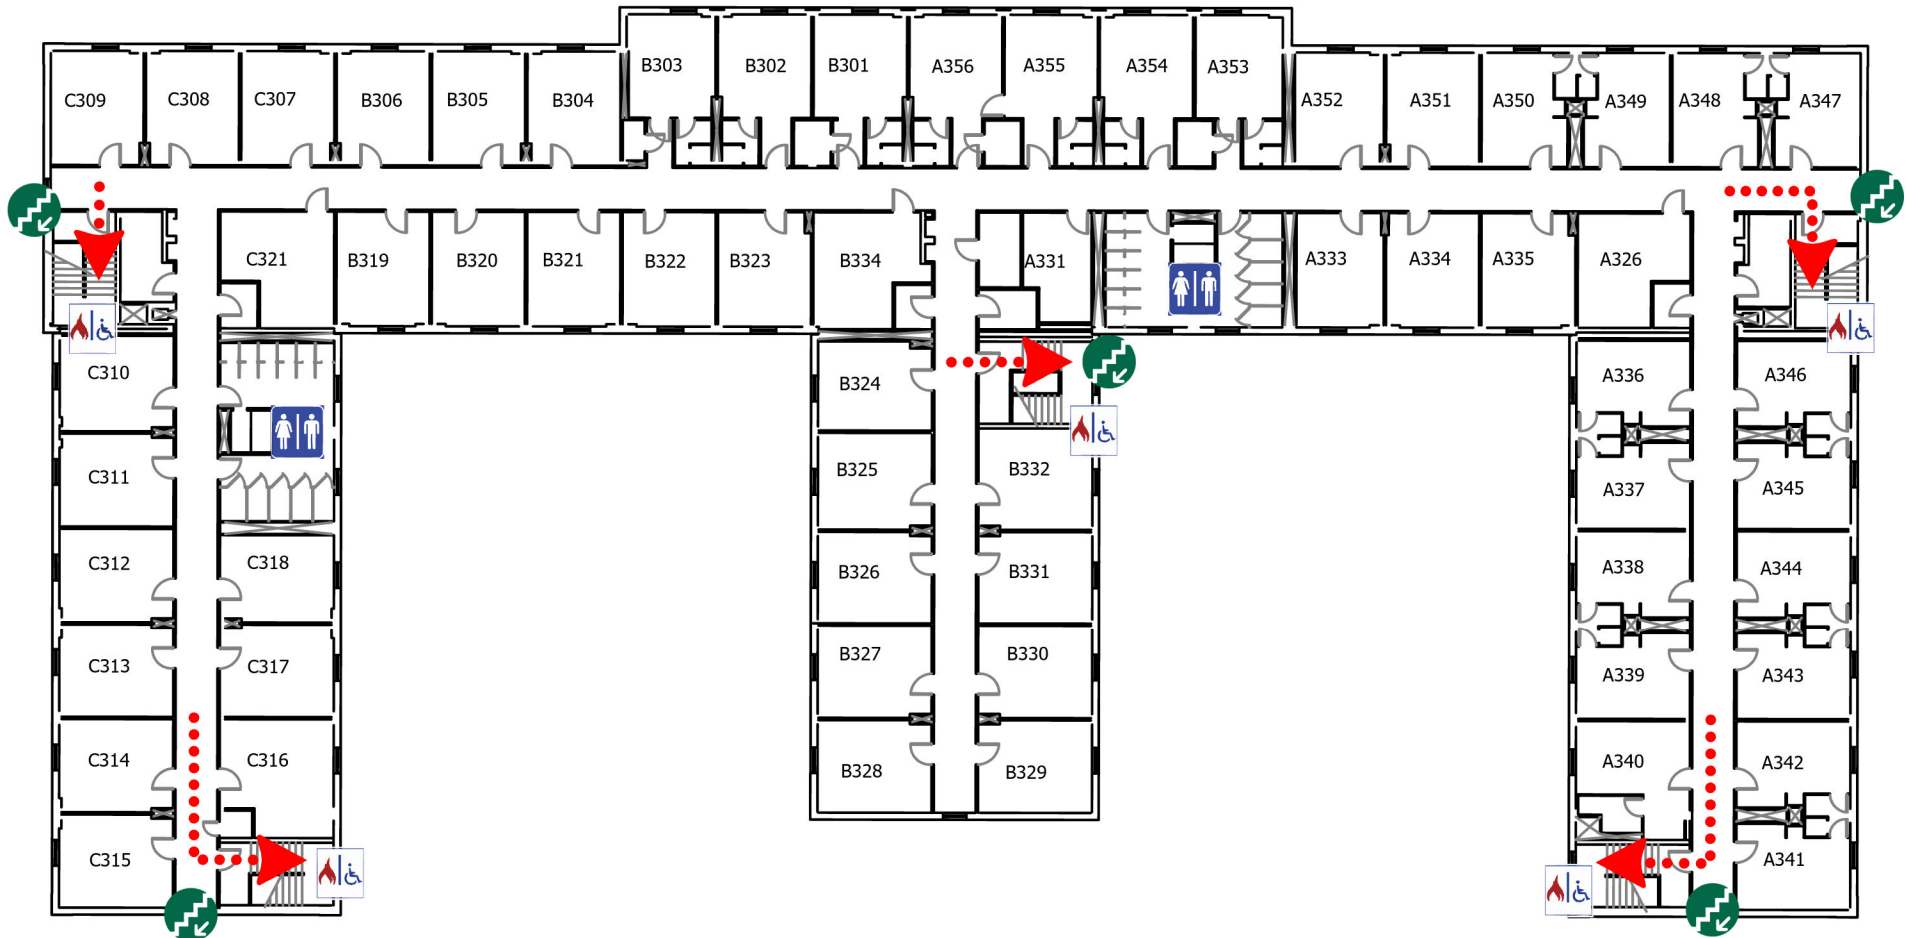

Stairs



Restroom



Refuge Area



Exit