


CLARK HALL FIRST FLOOR

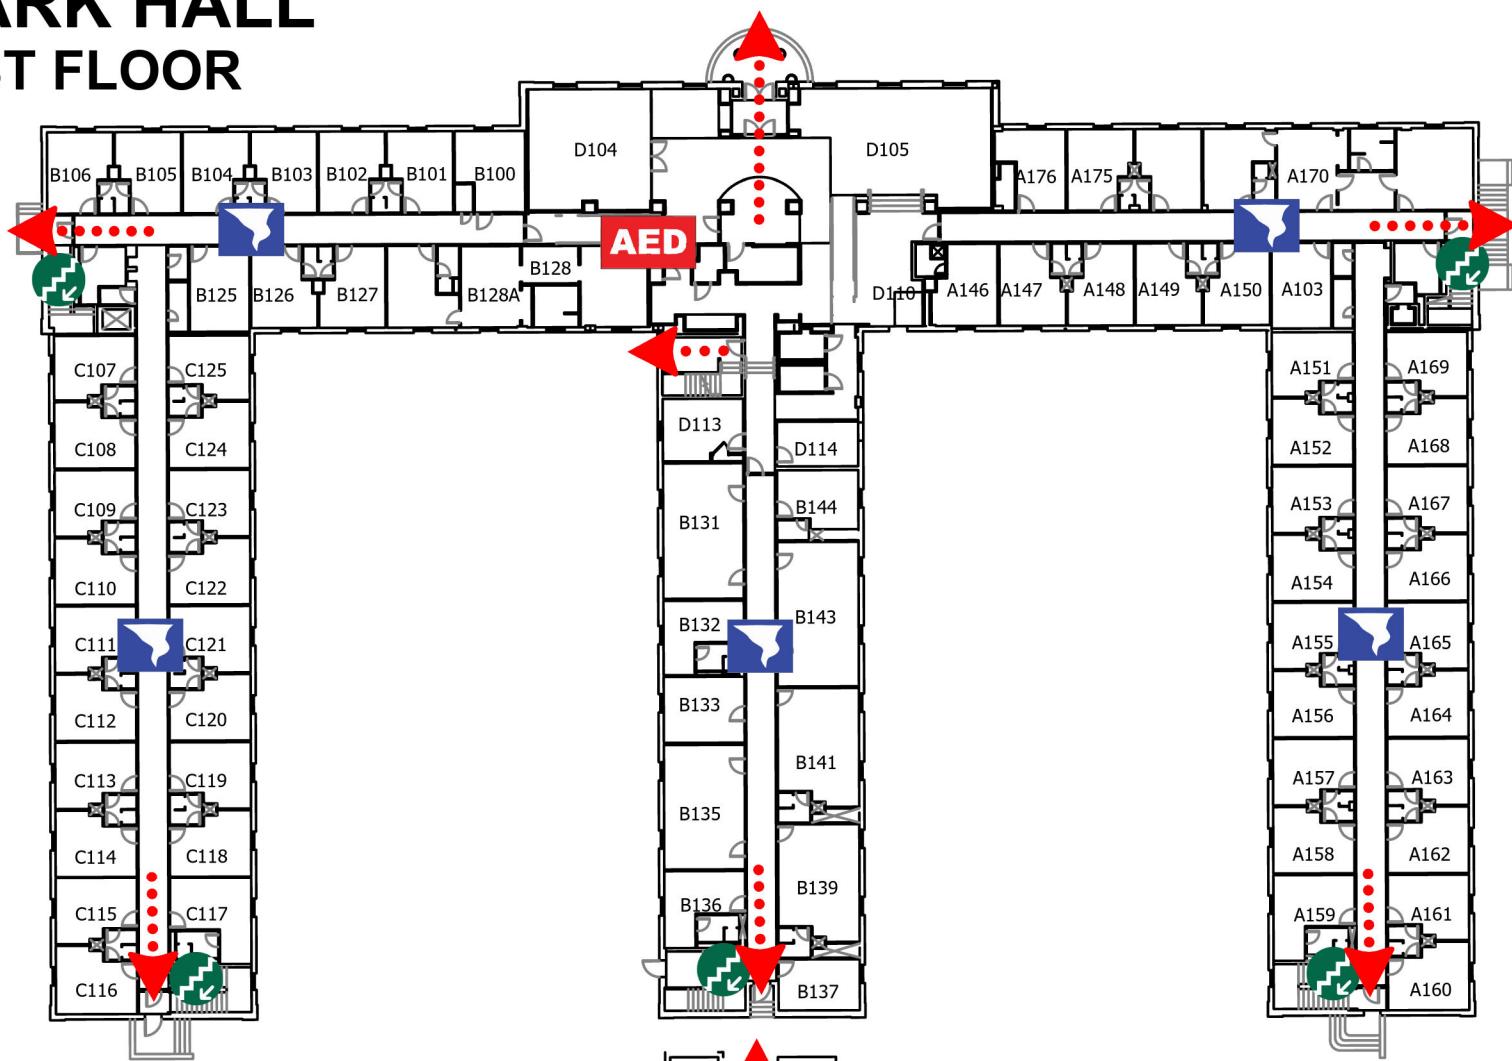

CLARK HALL SECOND FLOOR



Stairs




Refuge Area



Exit

CLARK HALL

THIRD FLOOR

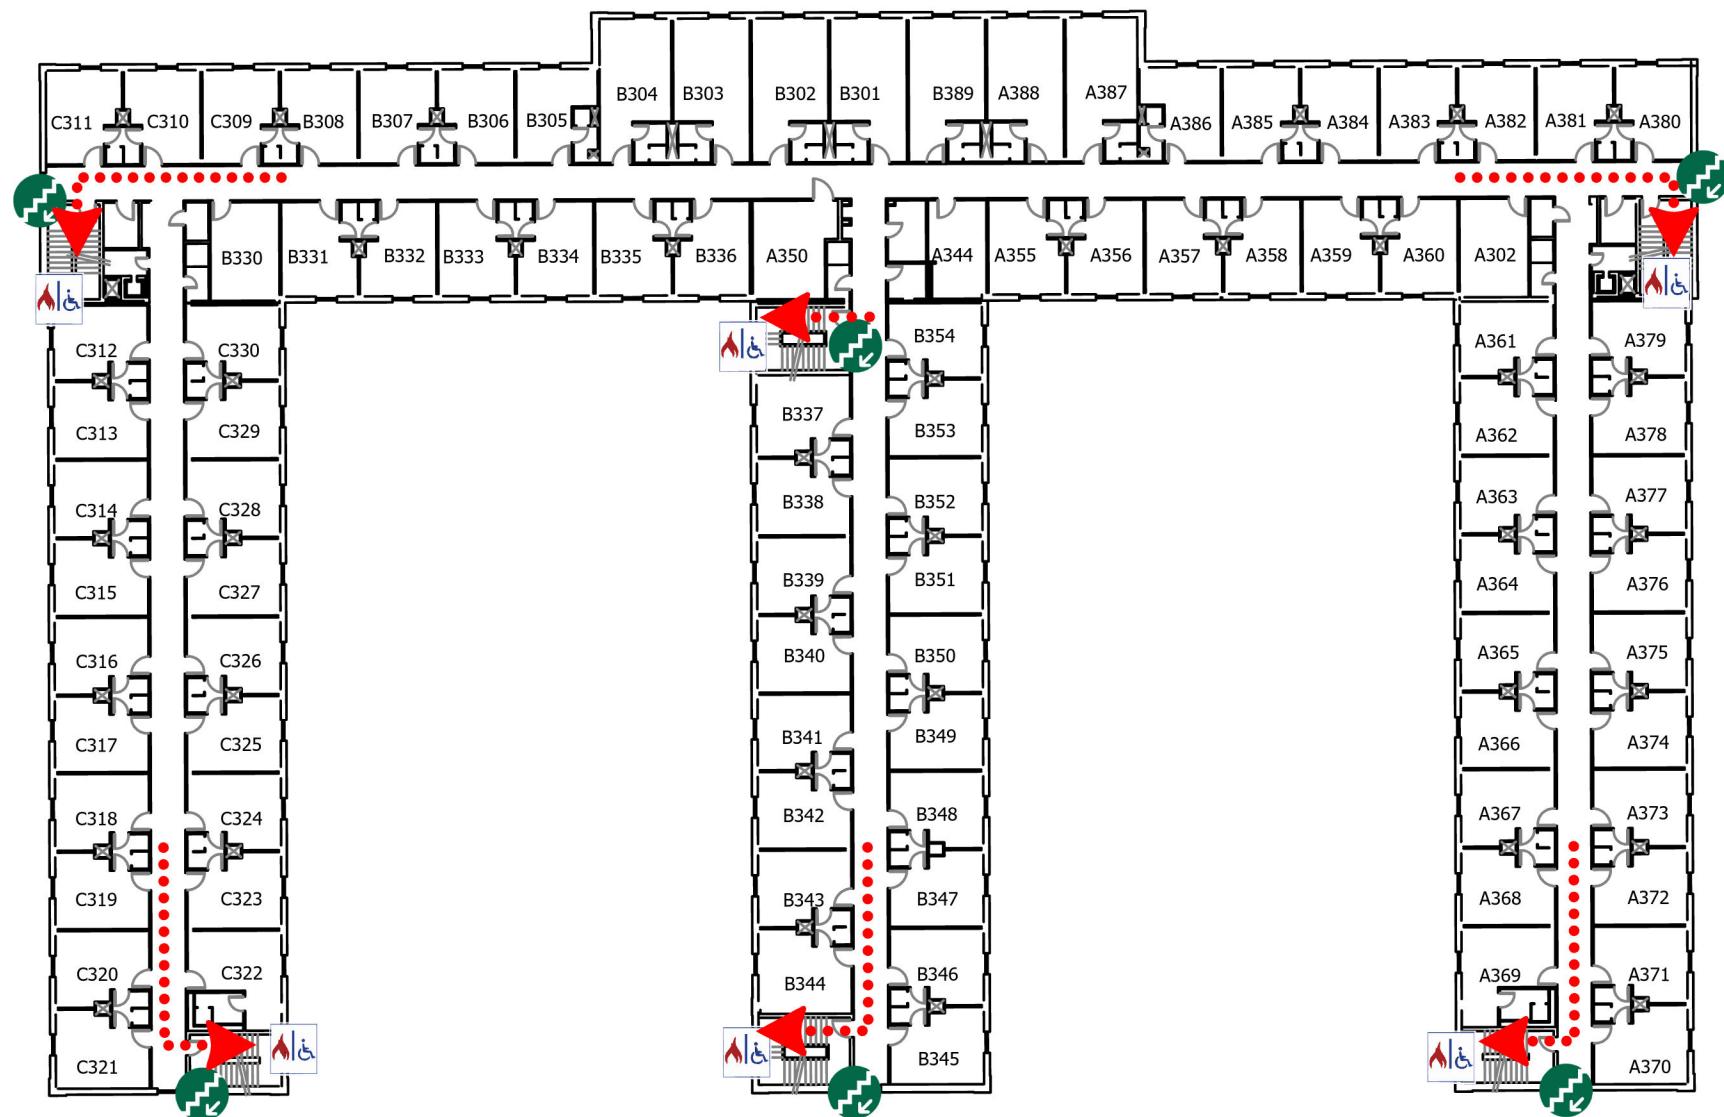

Stairs



Refuge Area



Exit