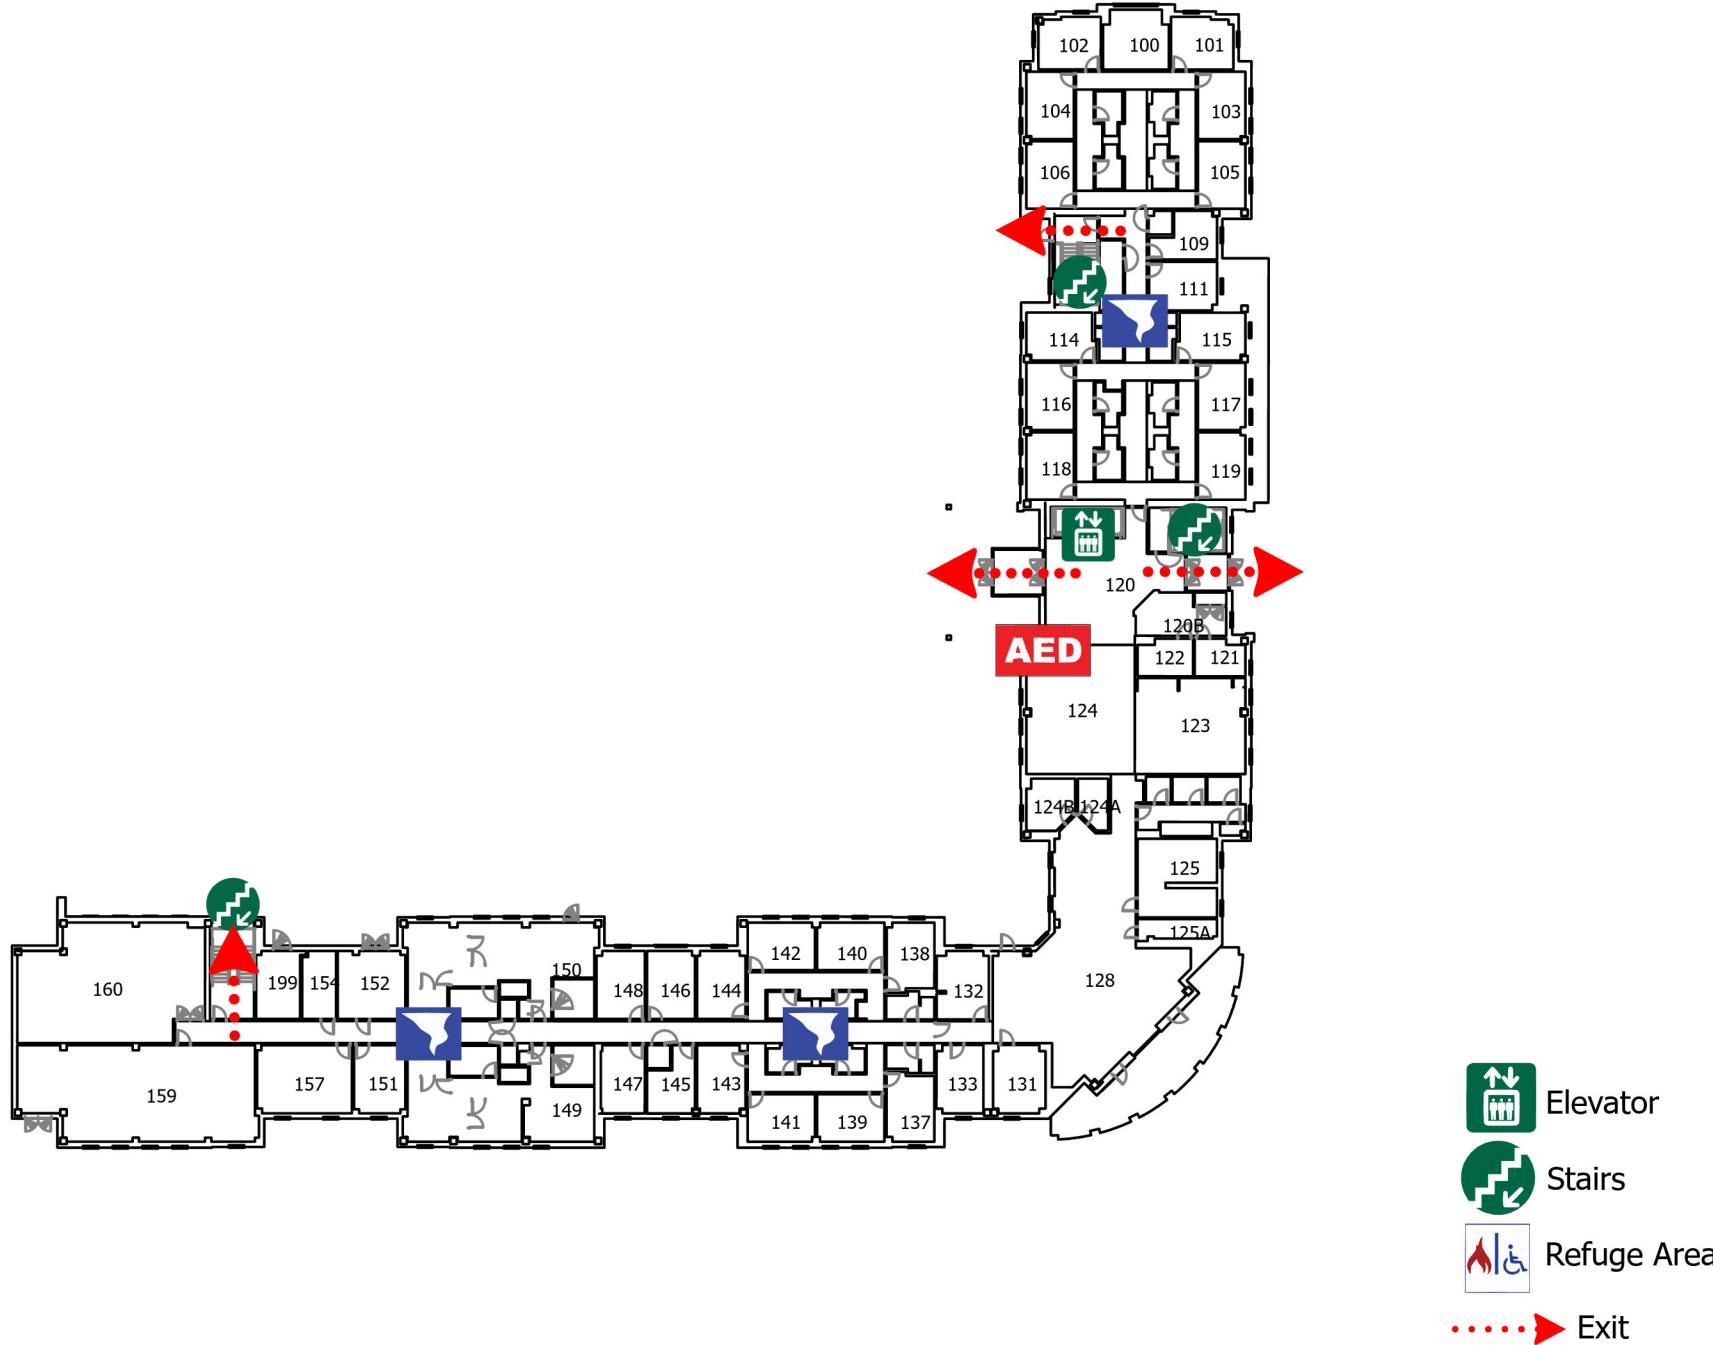


# JOE GREENE HALL

## FIRST FLOOR


N  

# JOE GREENE HALL

## SECOND FLOOR

N  

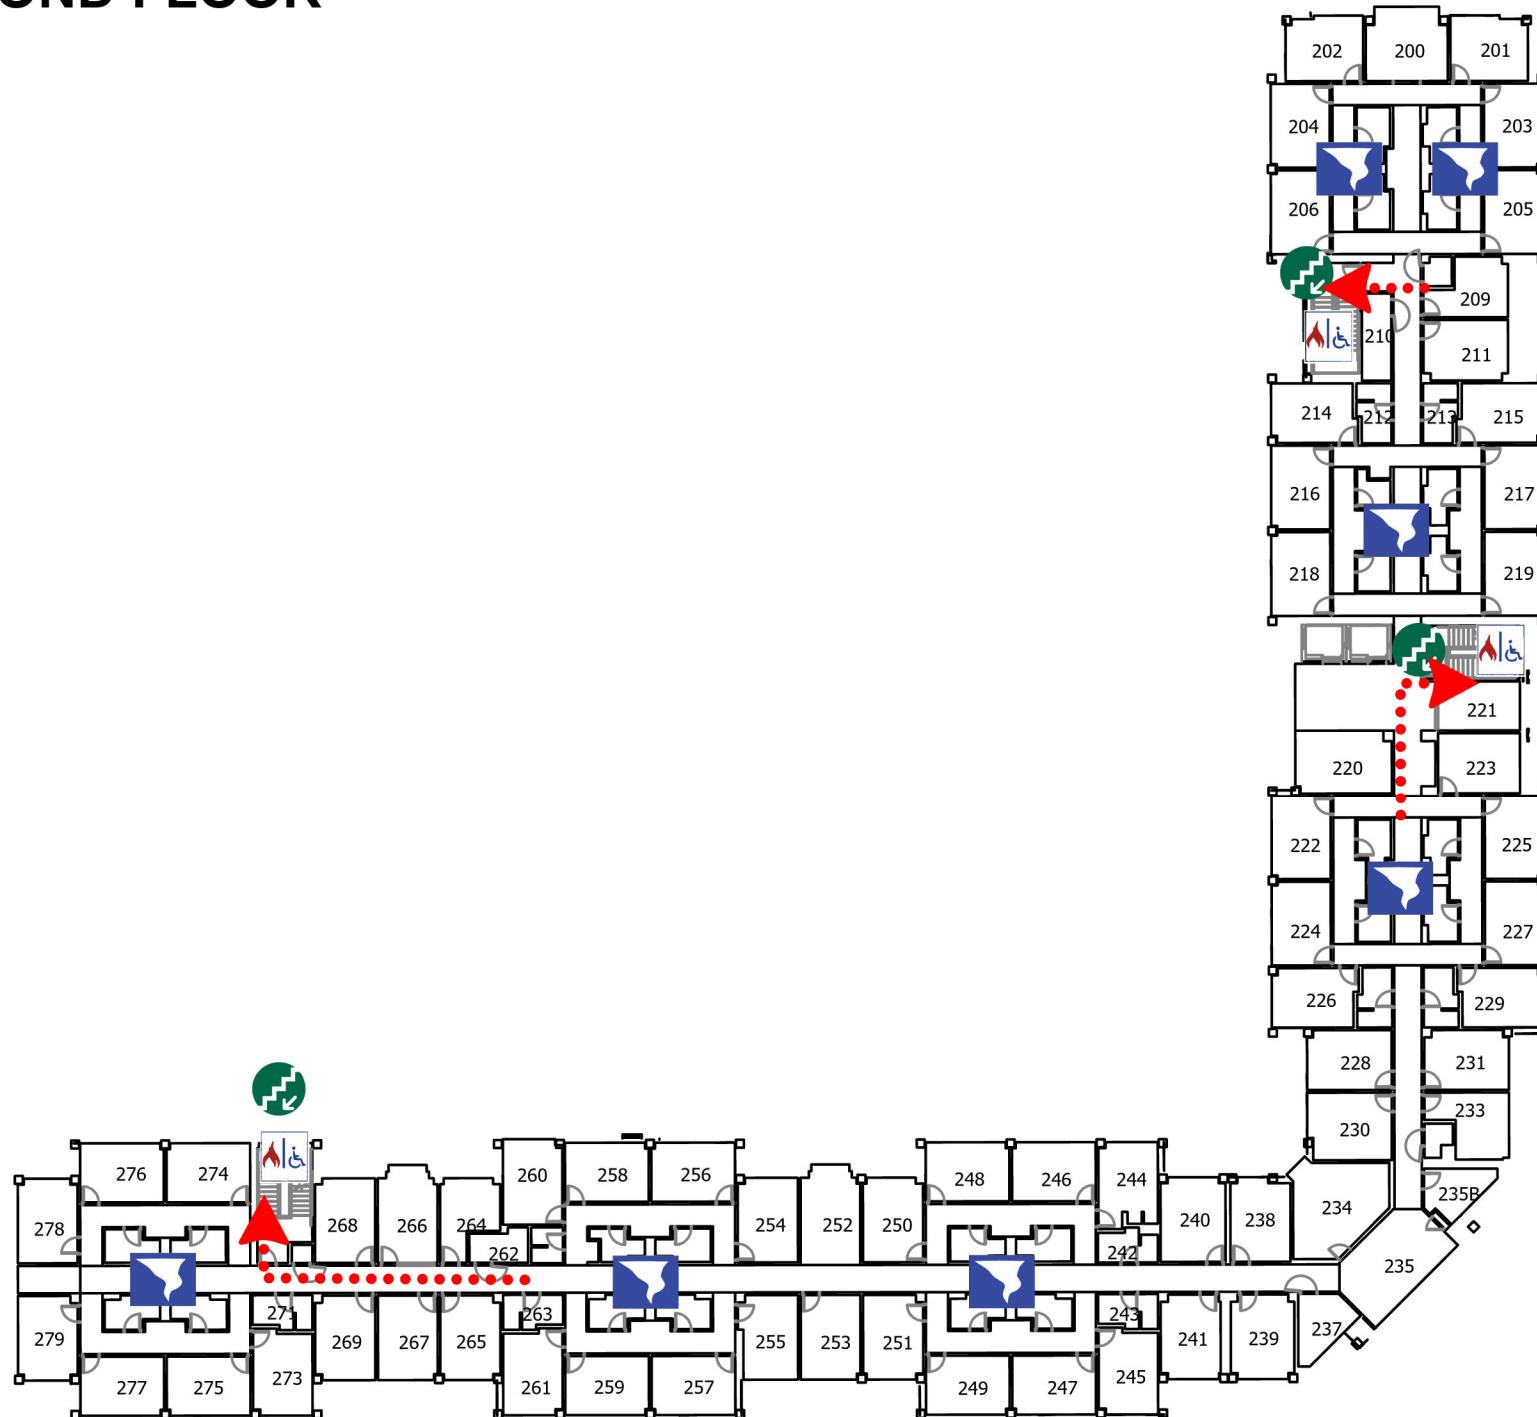



-  Elevator
-  Stairs
-  Shelter Area
-  Refuge Area
-  Exit

# JOE GREENE HALL

## THIRD FLOOR

N  

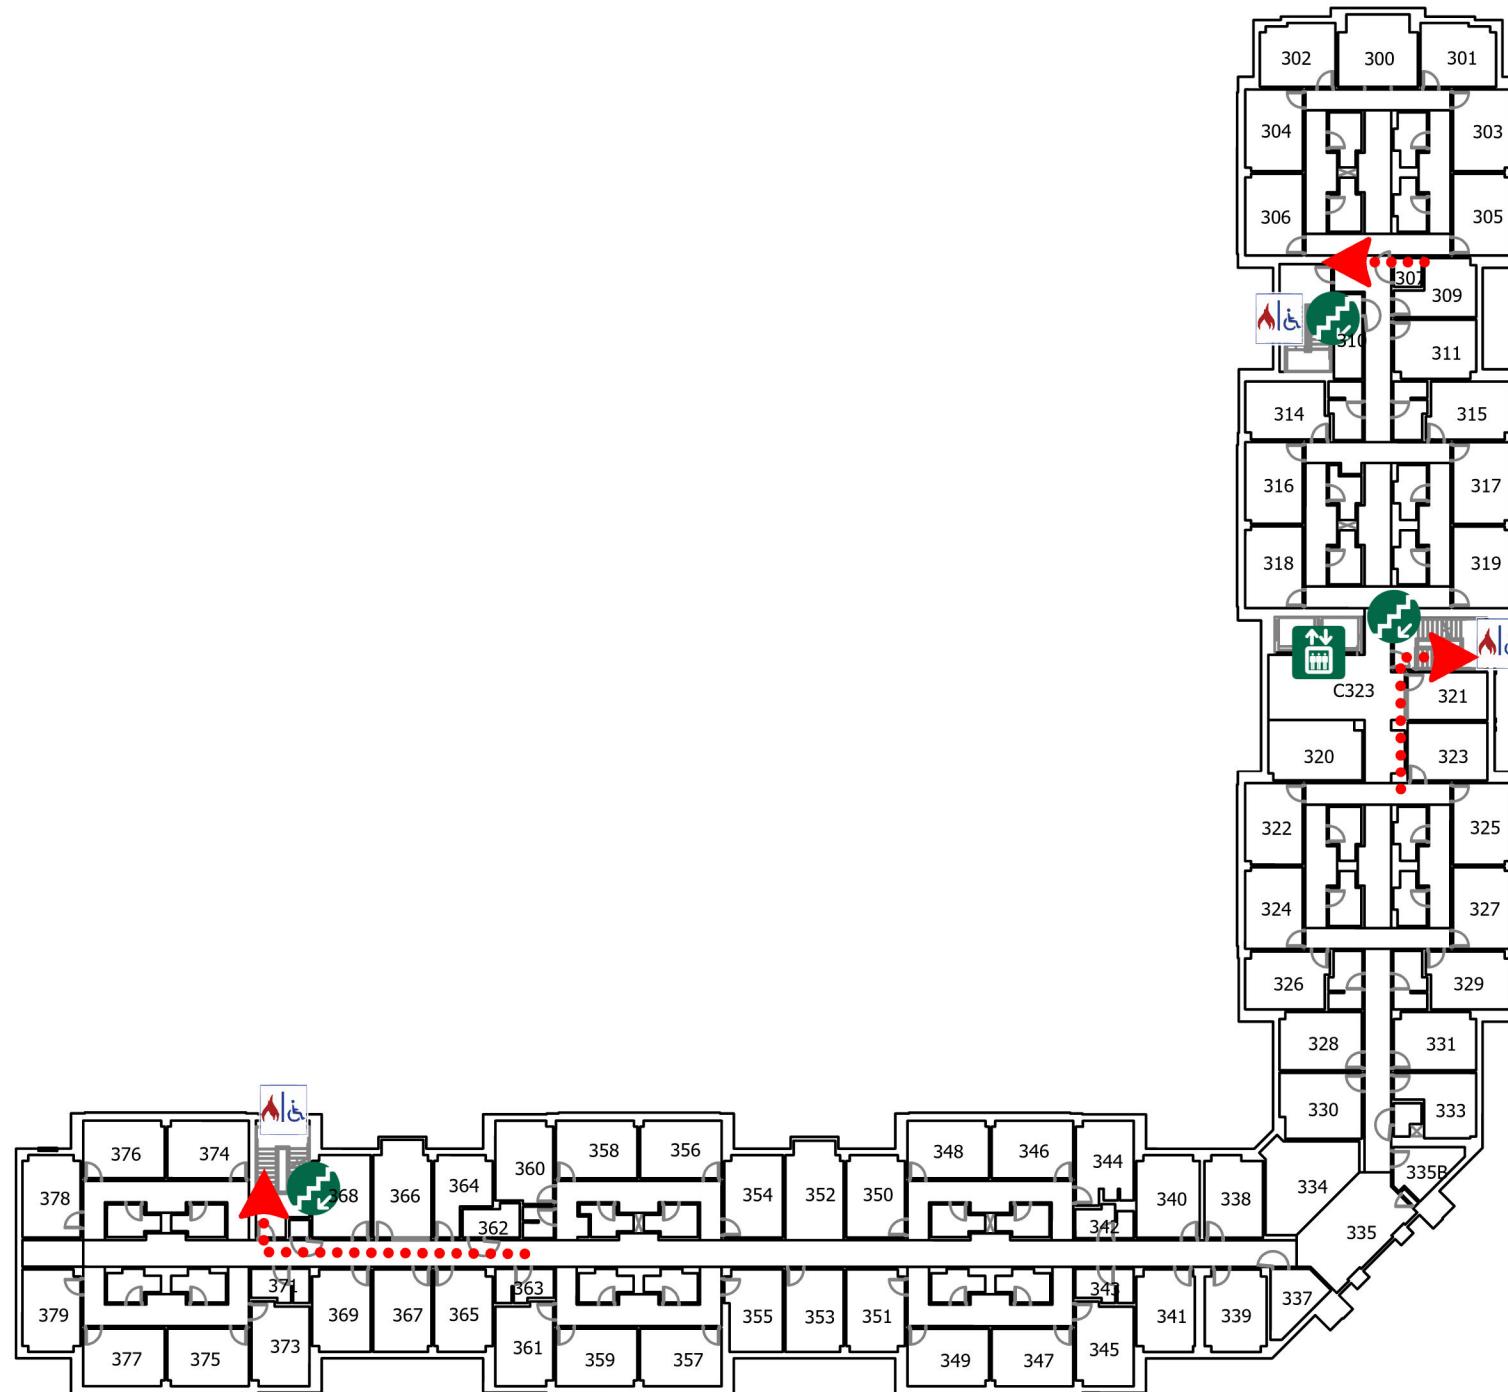-  Elevator
-  Stairs
-  Refuge Area
-  Exit