


CHESTNUT HALL

FIRST FLOOR

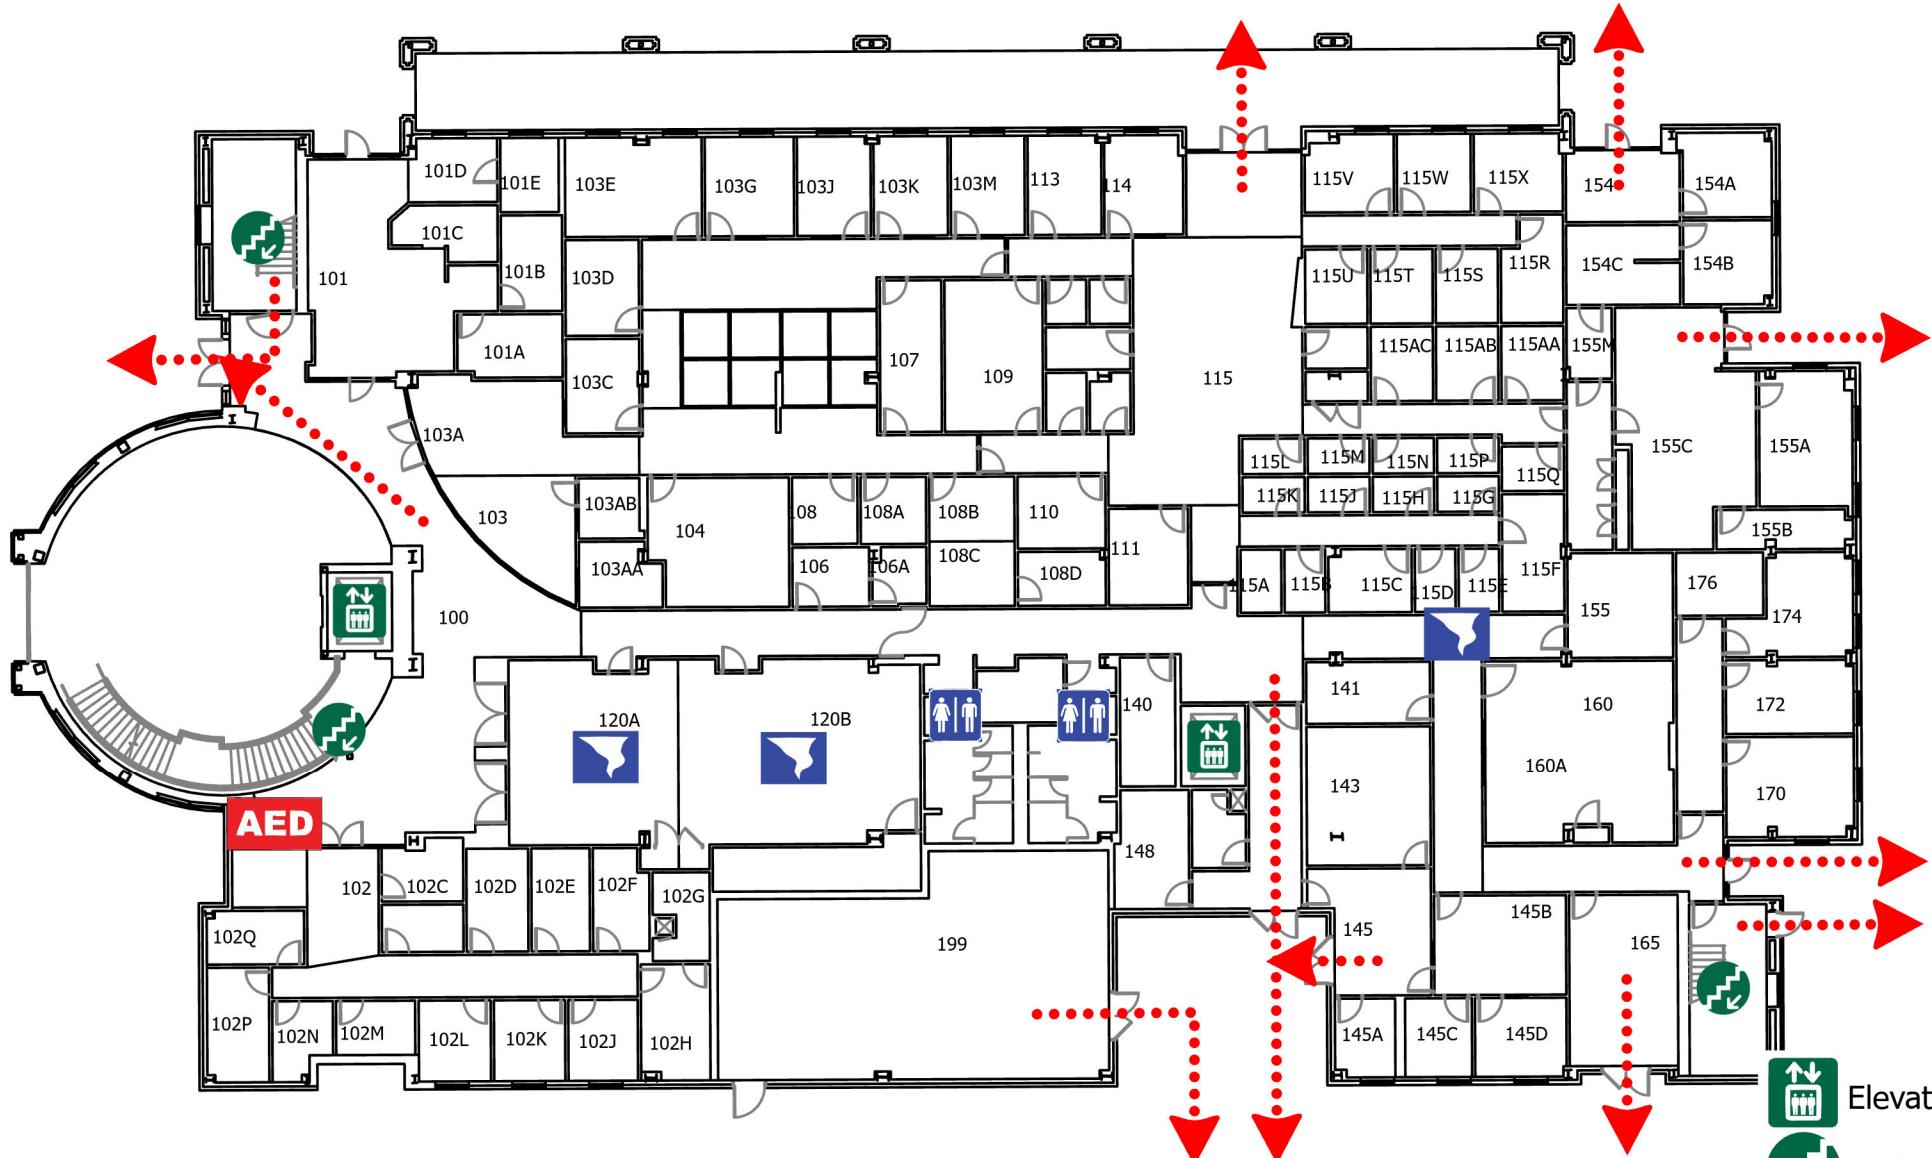

Elevator

Stairs


Shelter Area

Restroom

AED

Exit

CHESTNUT HALL SECOND FLOOR

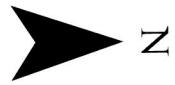

Elevator



Stairs



Restroom




Refuge Area

AED

Exit

CHESTNUT HALL

THIRD FLOOR

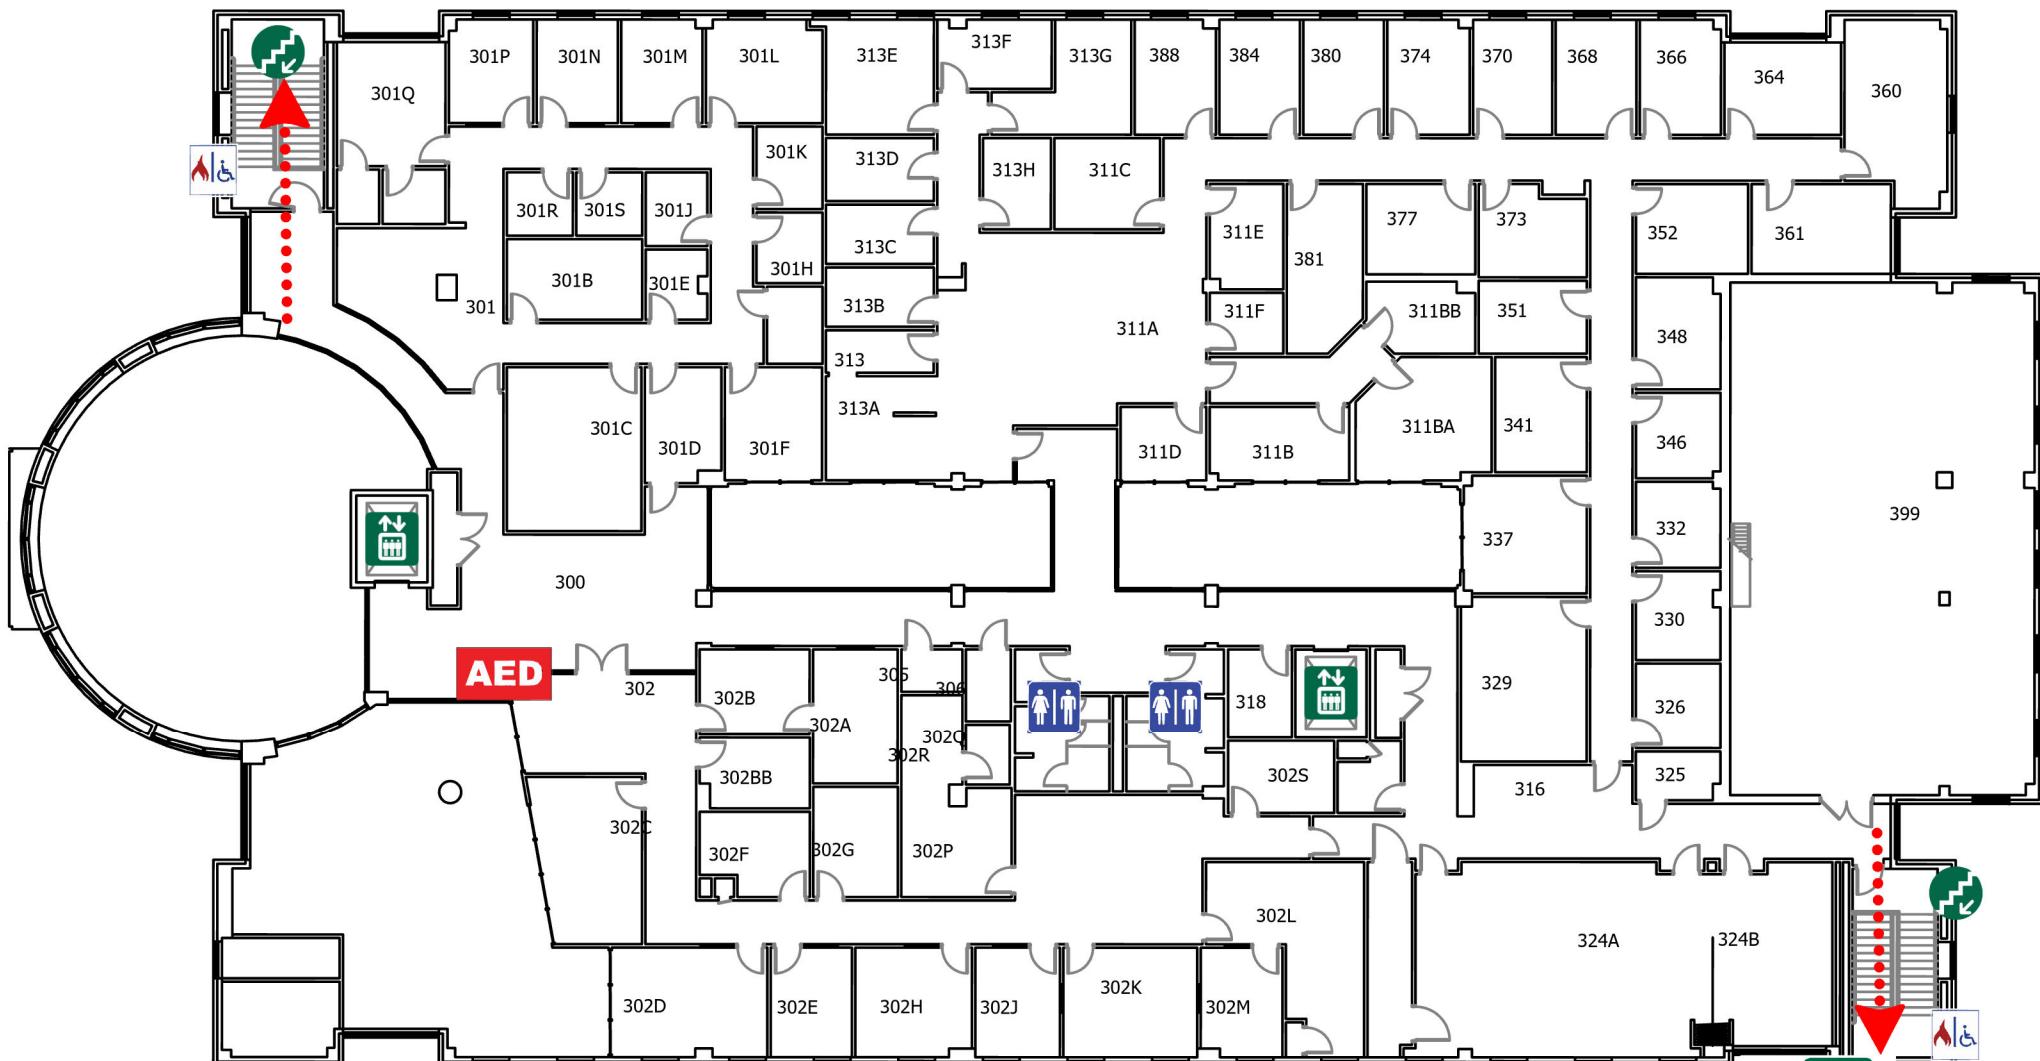

- Elevator
- Stairs
- Restroom
- Refuge Area

AED AED

Exit