



# TRADITIONS HALL

## FIRST FLOOR

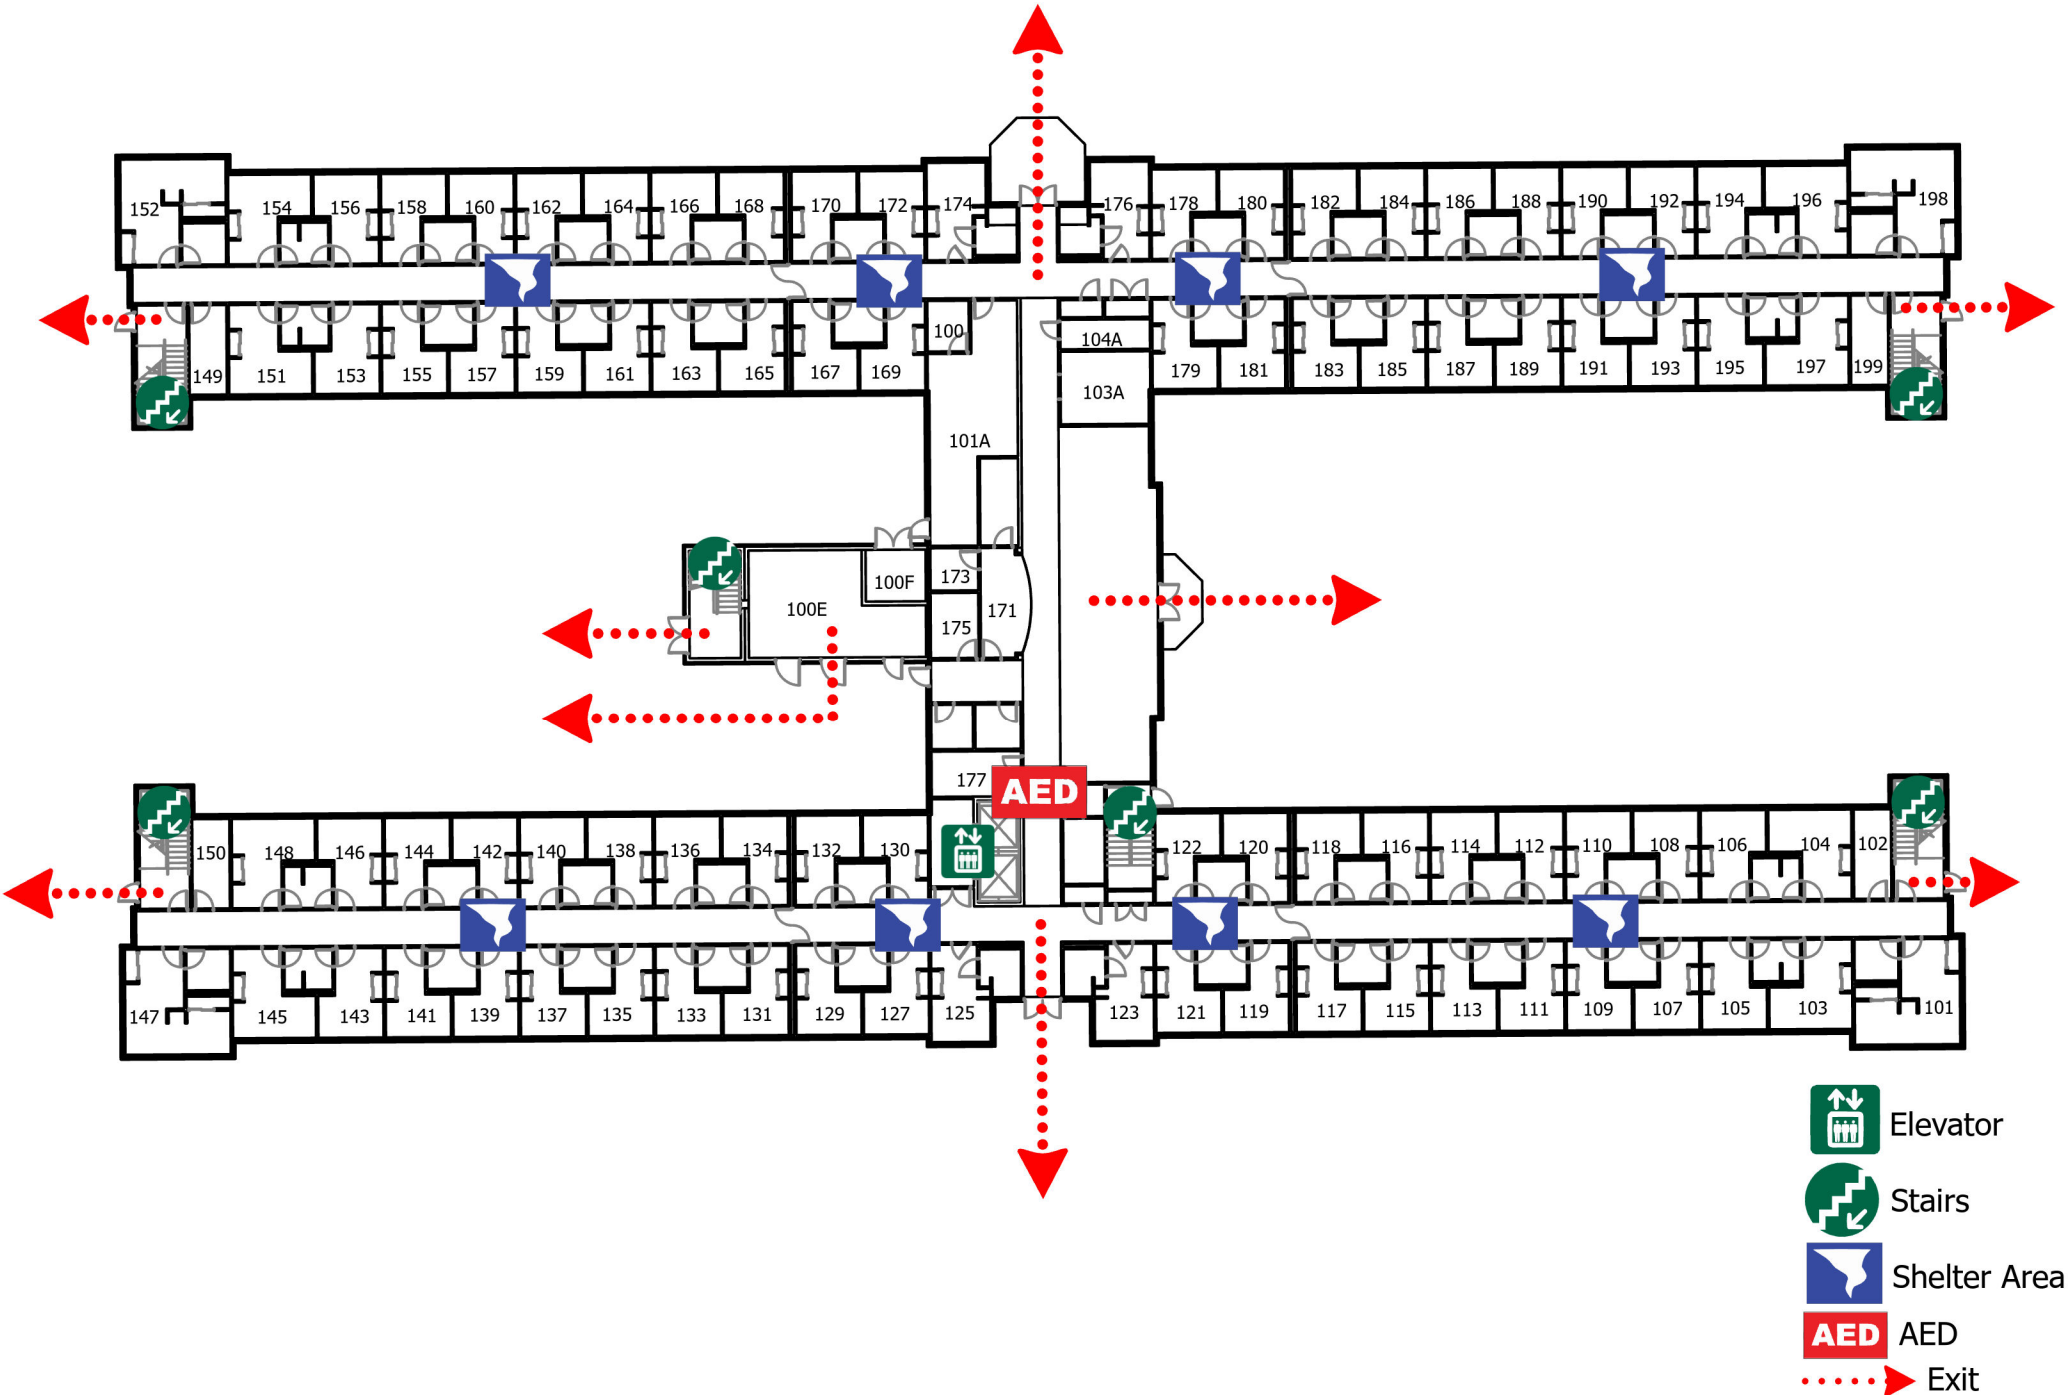

# TRADITIONS HALL


## SECOND FLOOR

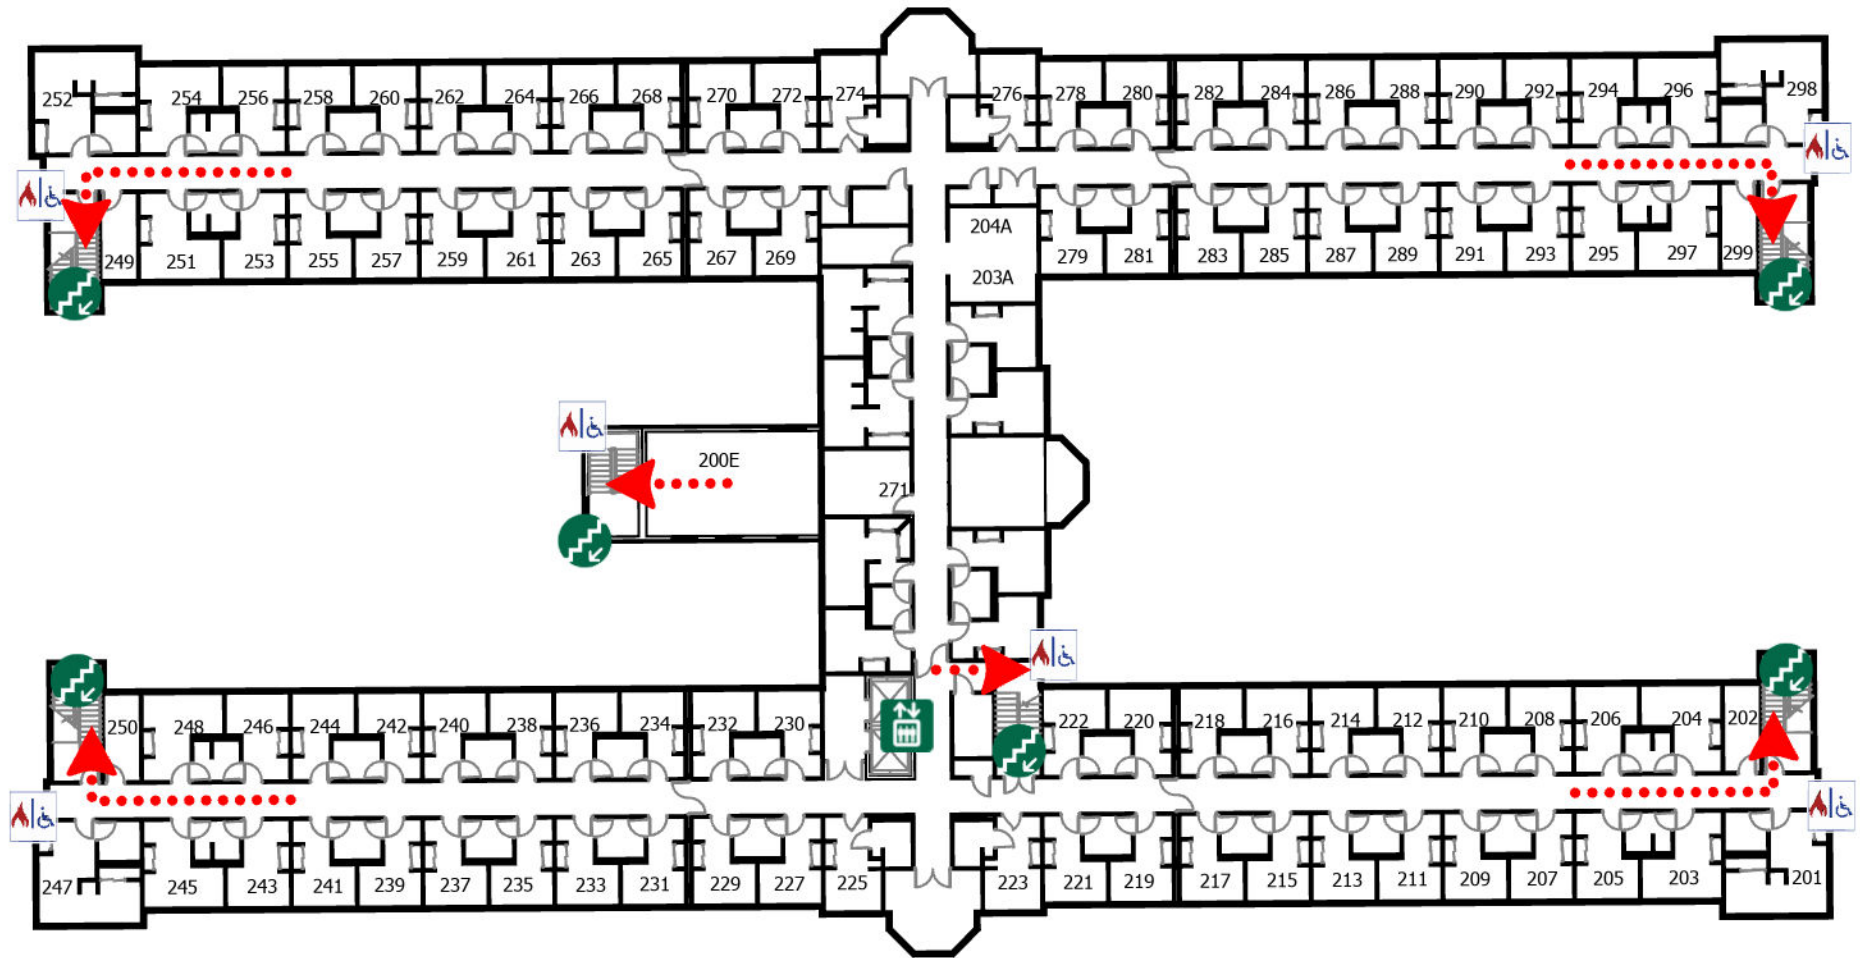

-  Elevator
-  Stairs
-  Refuge Area
-  Exit

# TRADITIONS HALL

## THIRD FLOOR

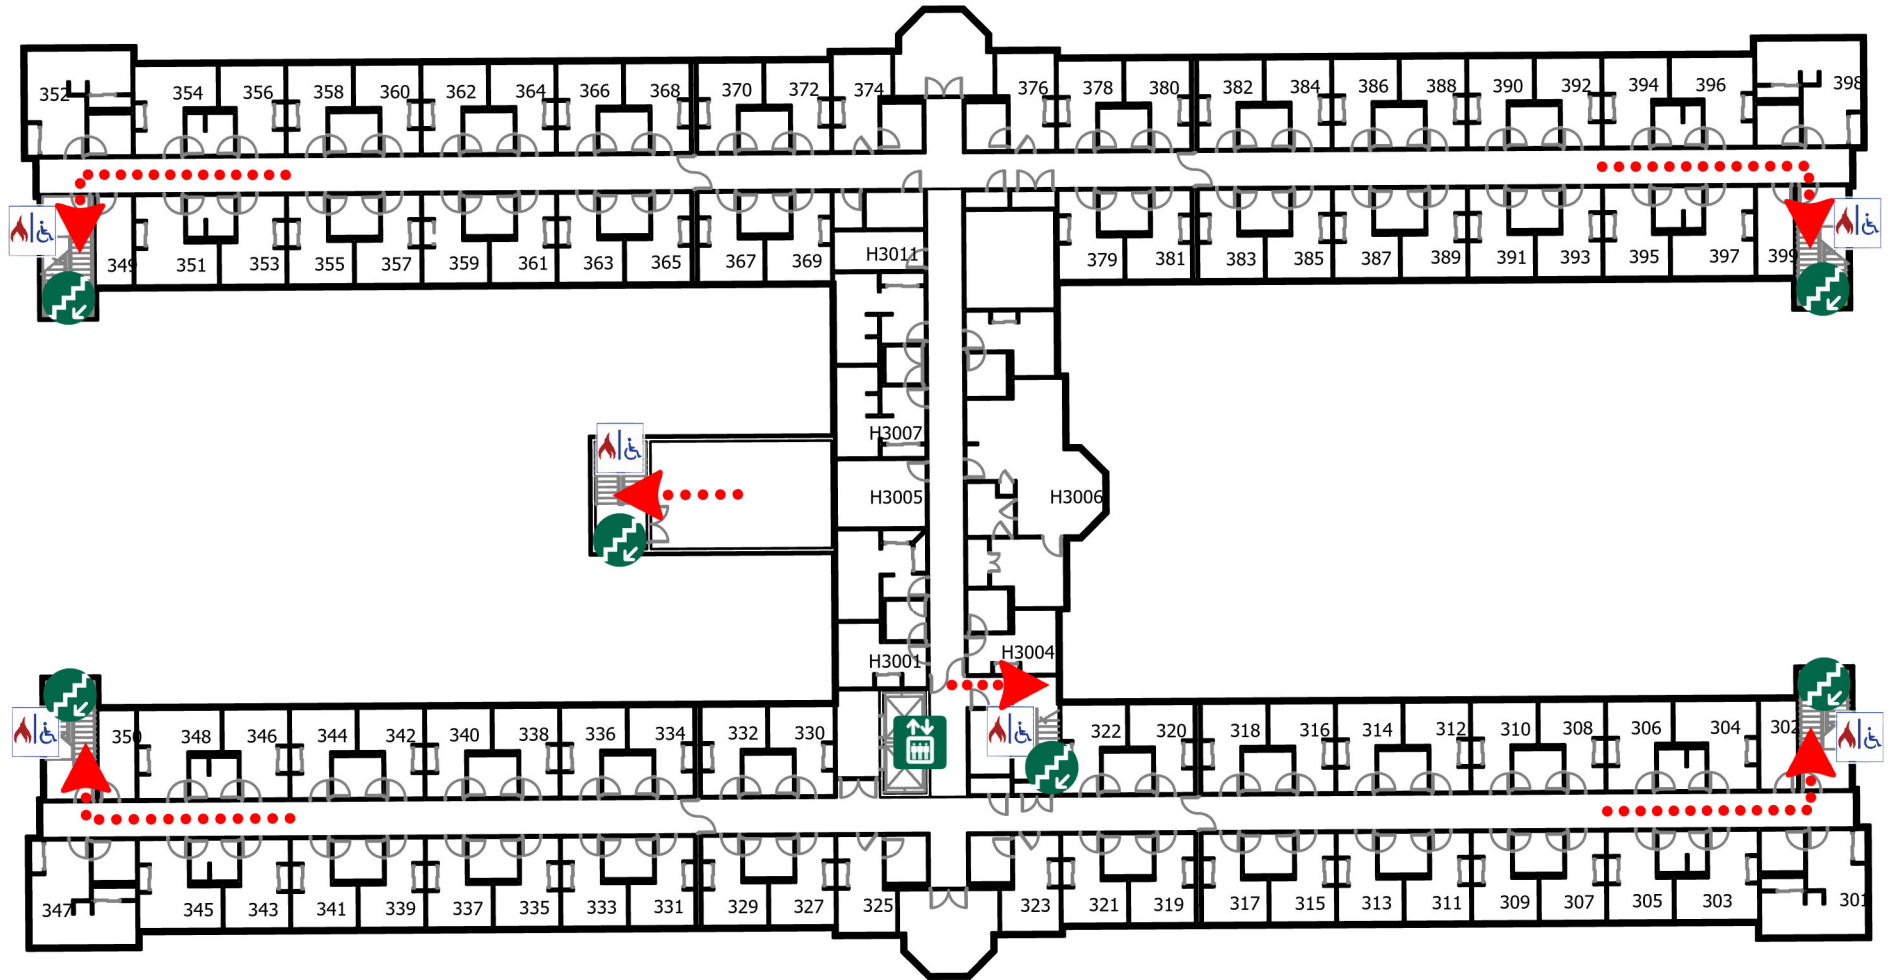

-  Elevator
-  Stairs
-  Refuge Area
-  Exit