


# VICTORY HALL

## FIRST FLOOR

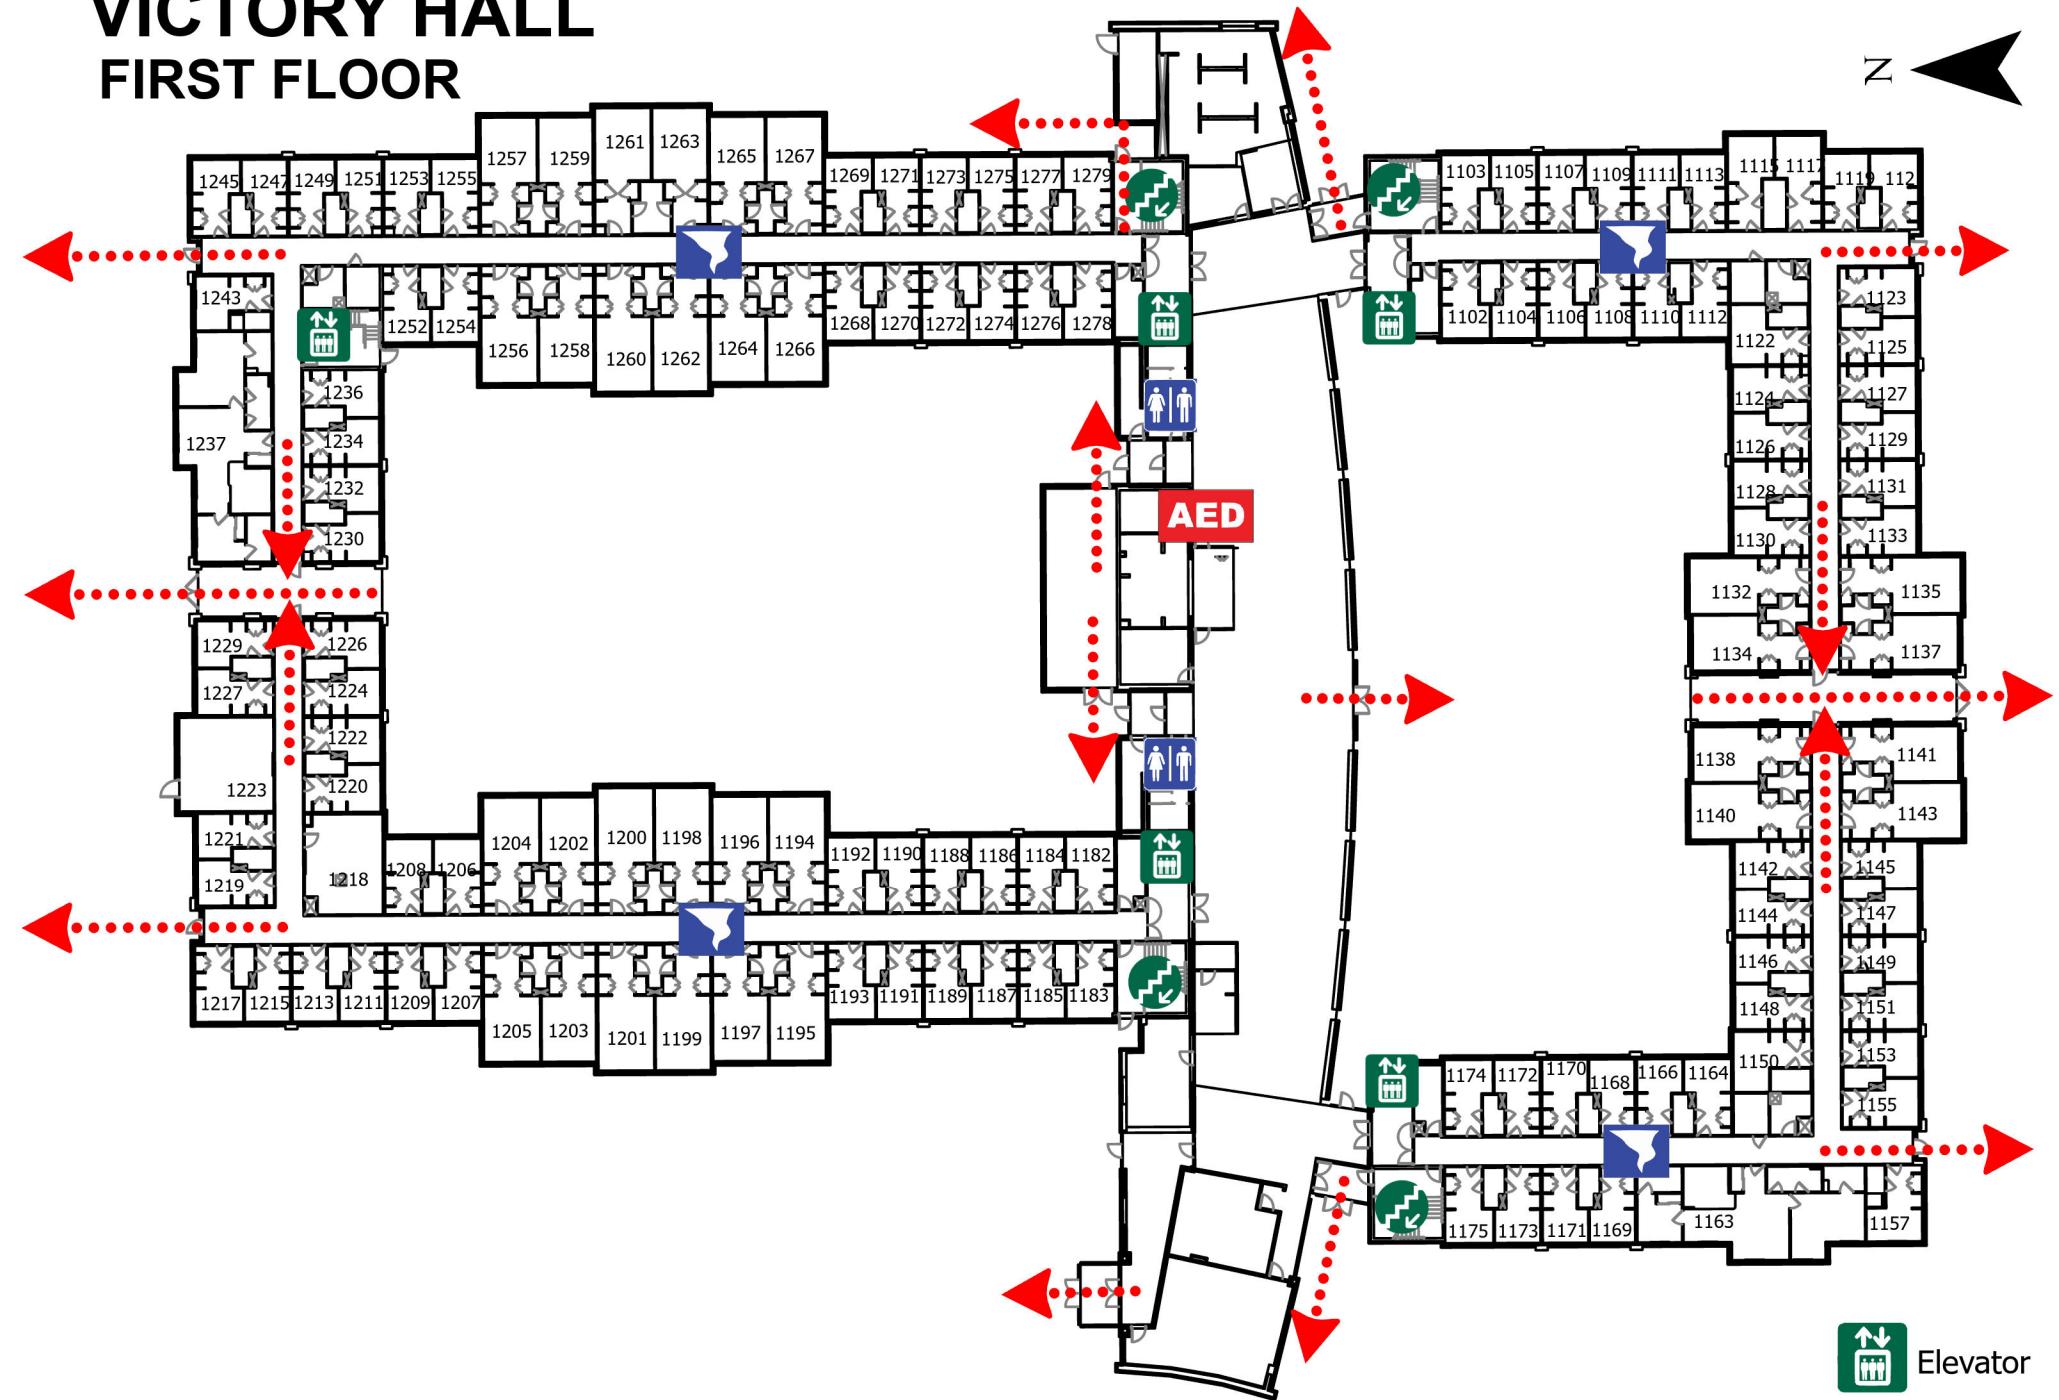

 Elevator

A blue square icon containing a white female figure on the left and a white male figure on the right, separated by a vertical line.

 Stairs



 Shelter Area

AED

.....  Exit

# VICTORY HALL


## SECOND FLOOR

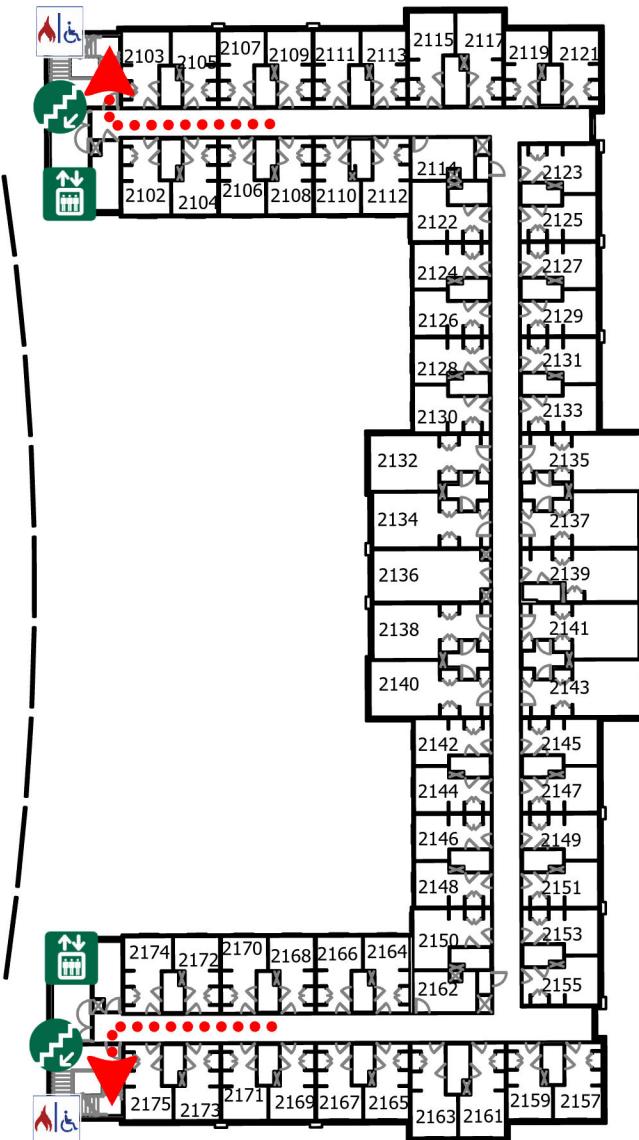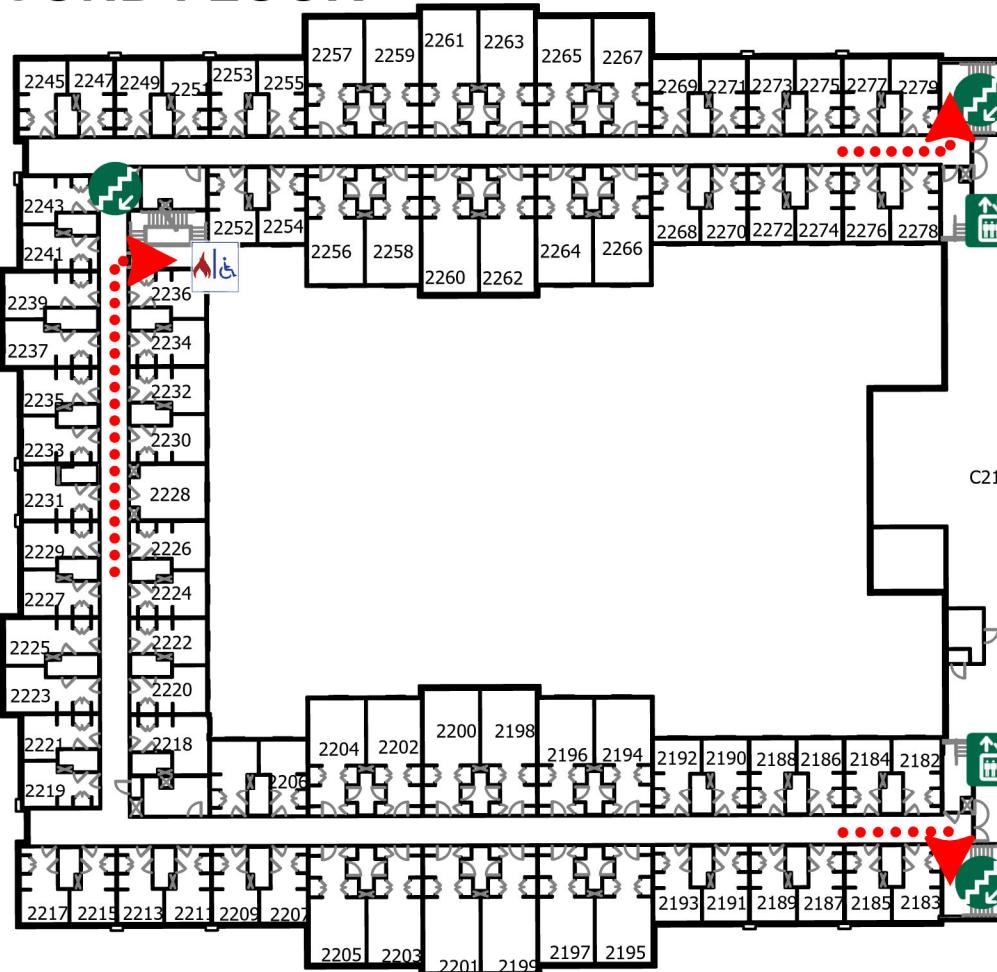

- Elevator
- Stairs
- Refuge Area
- Exit


# VICTORY HALL

## THIRD FLOOR

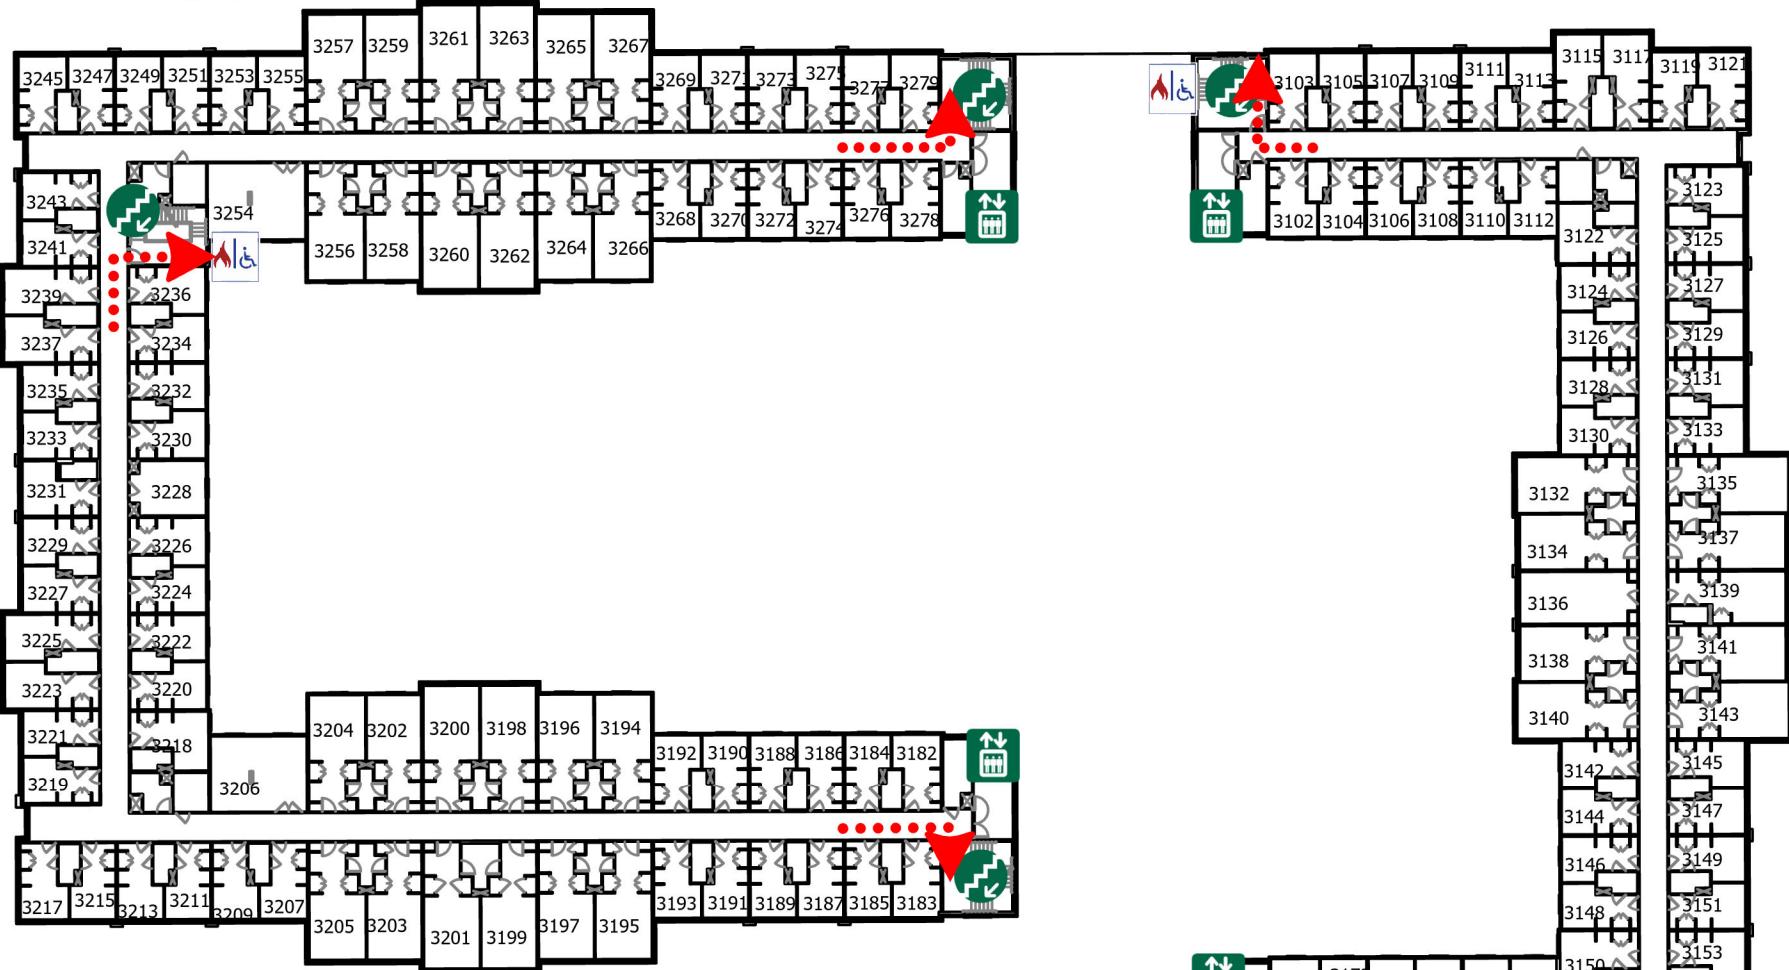

- Elevator
- Stairs
- Refuge Area
- Exit

# VICTORY HALL FOURTH FLOOR

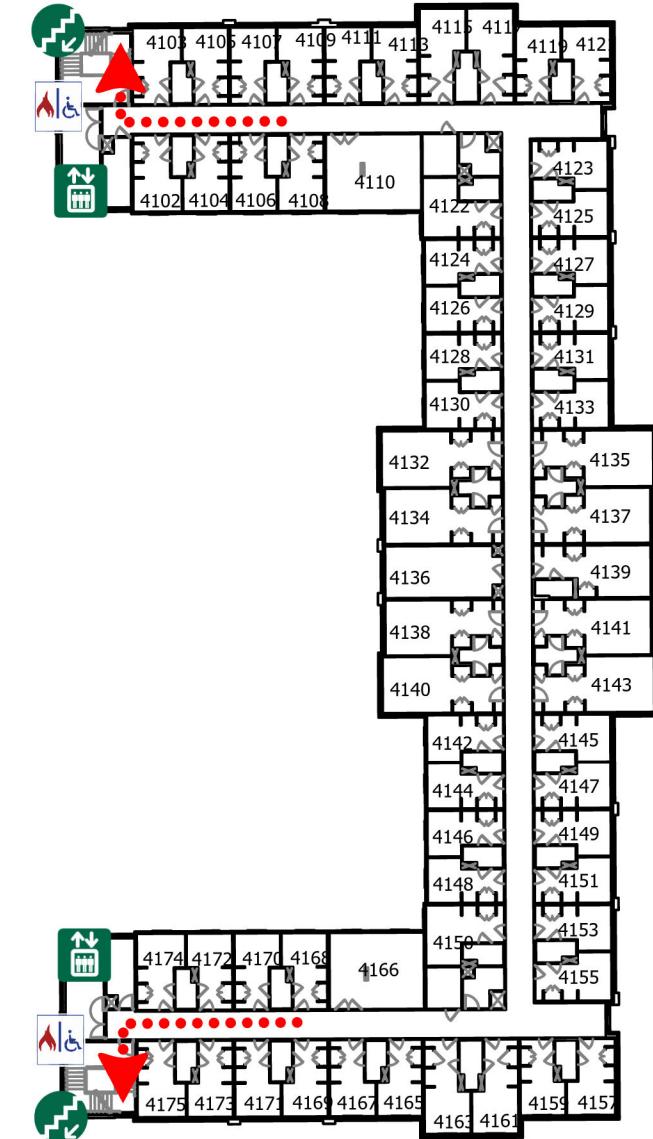

Elevator



F  
K Stairs



 Refuge Area



• •  Exit