


PHYSICS BUILDING


BASEMENT

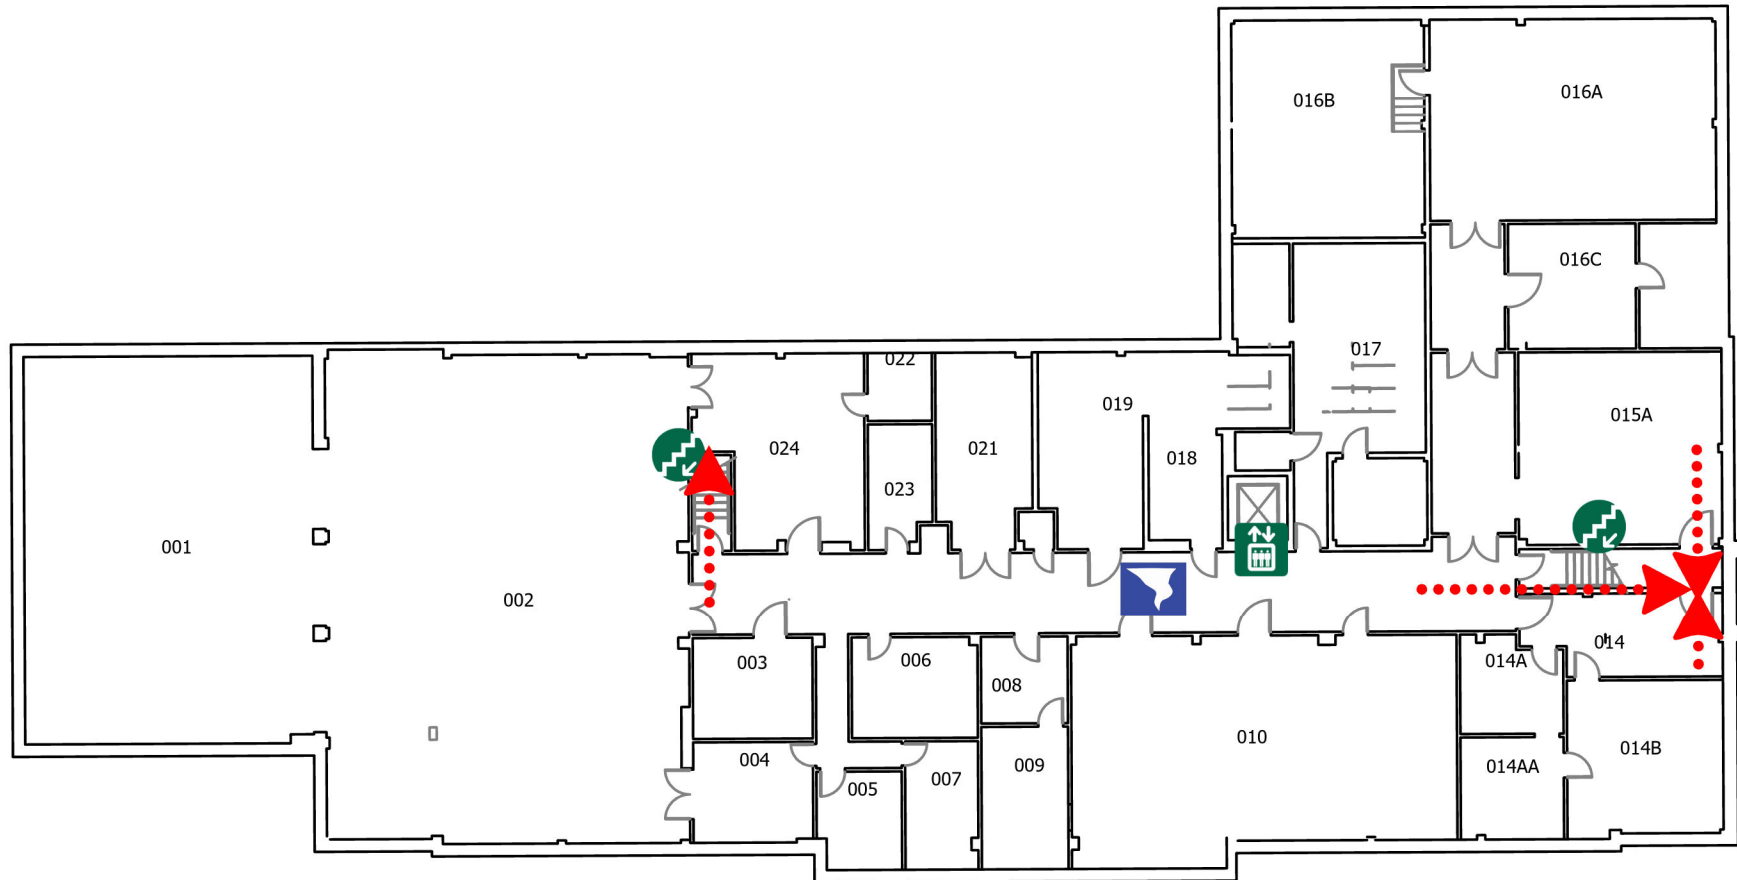

-  Elevator
-  Stairs
-  Shelter Area
-  Exit


PHYSICS BUILDING

FIRST FLOOR

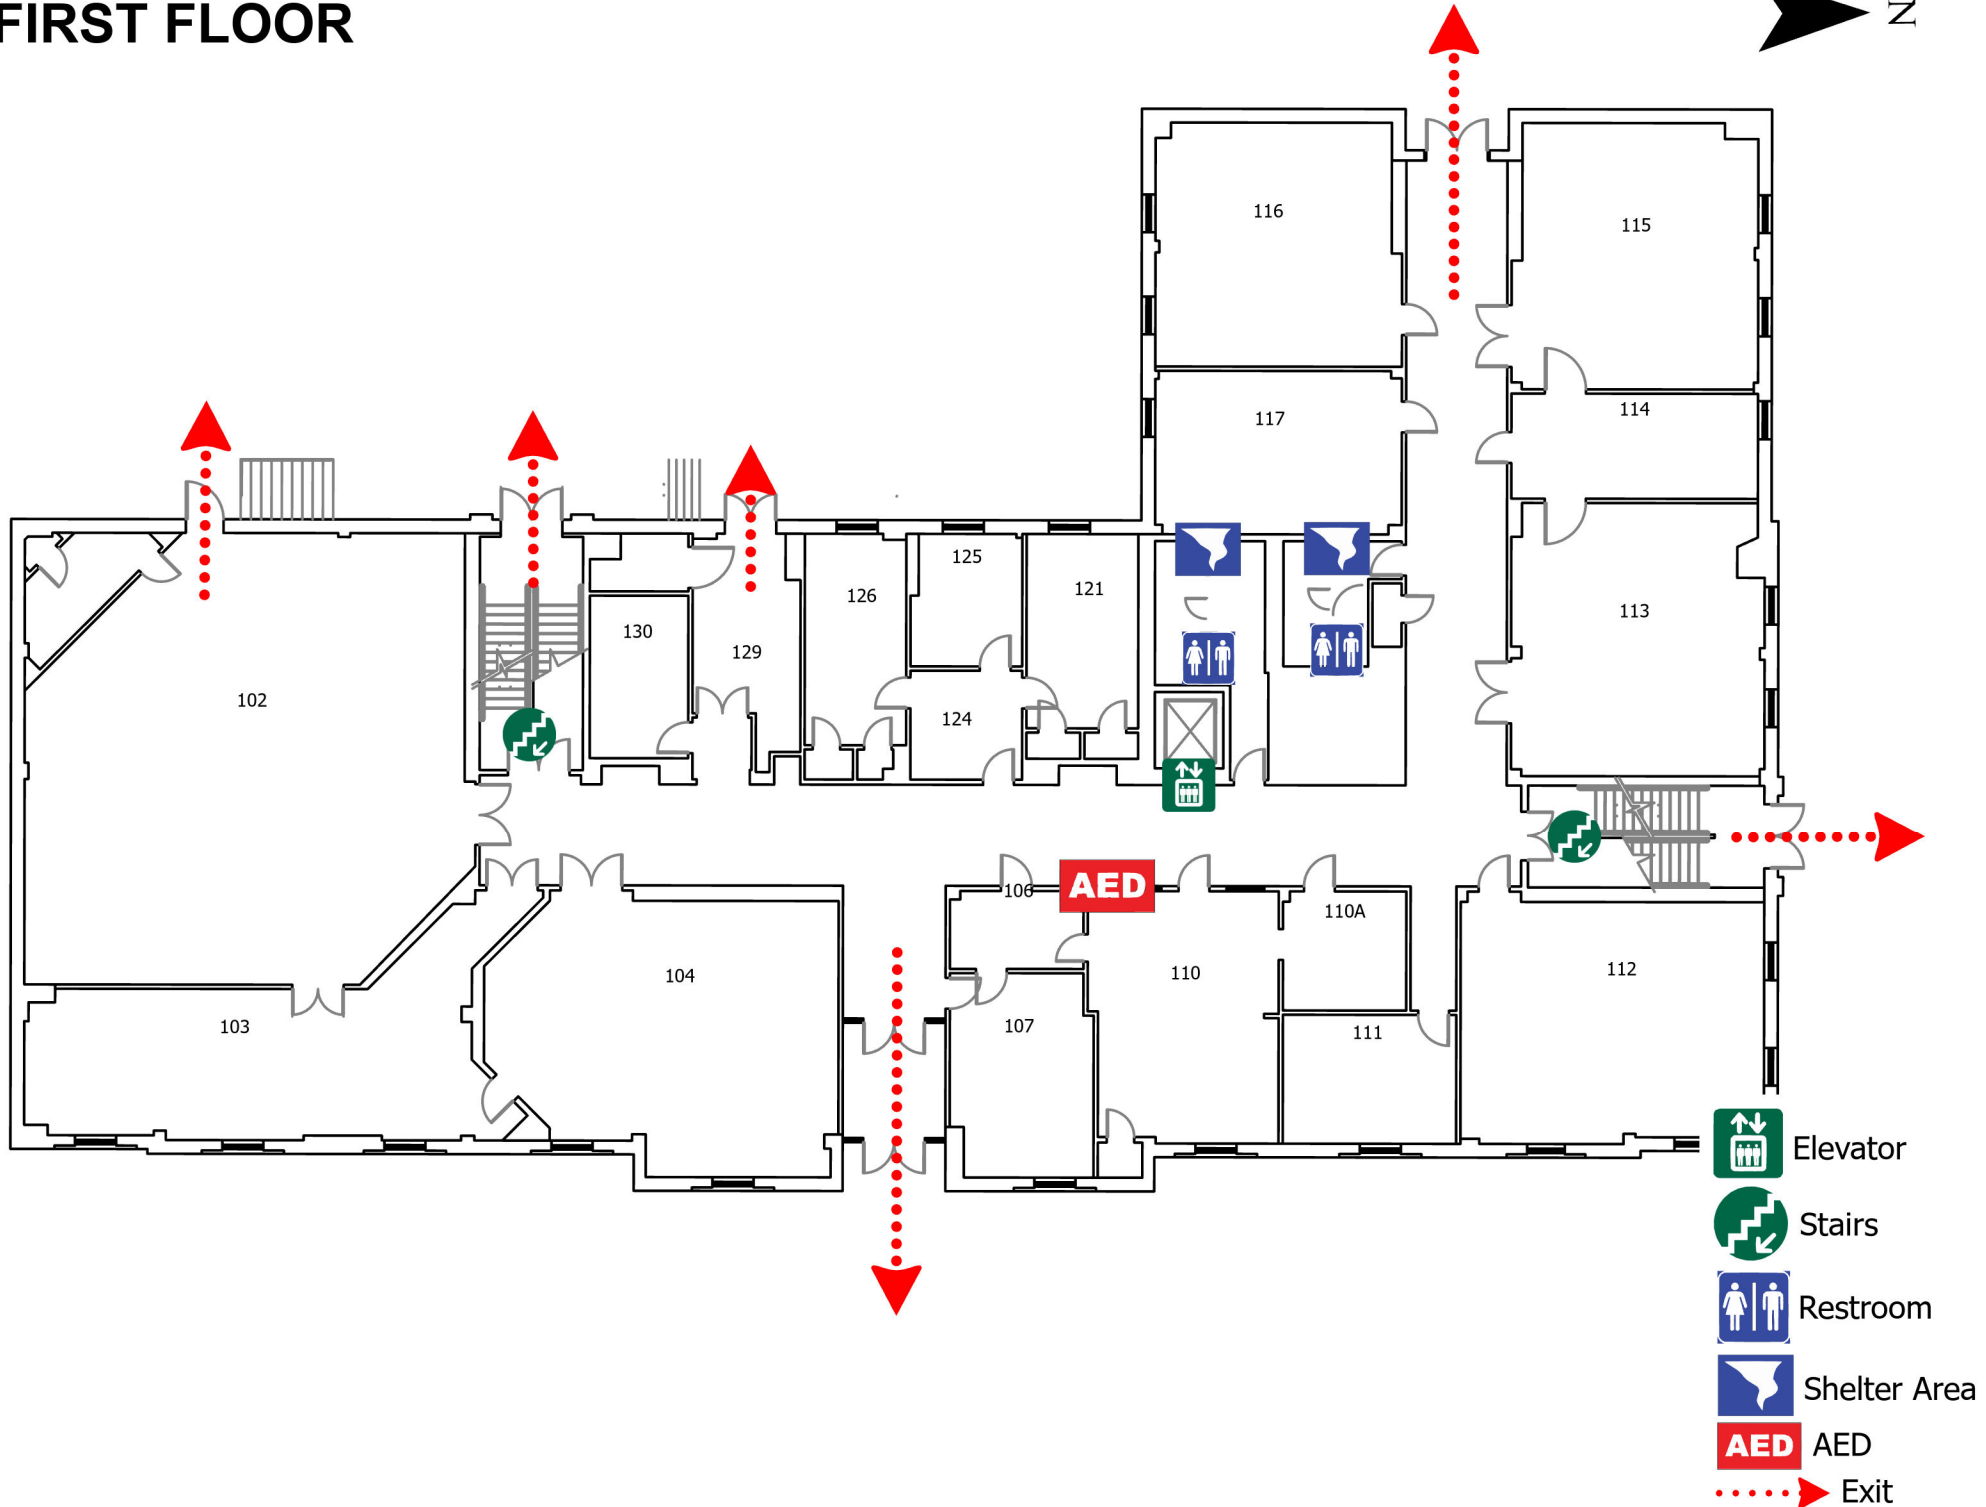

PHYSICS BUILDING

SECOND FLOOR

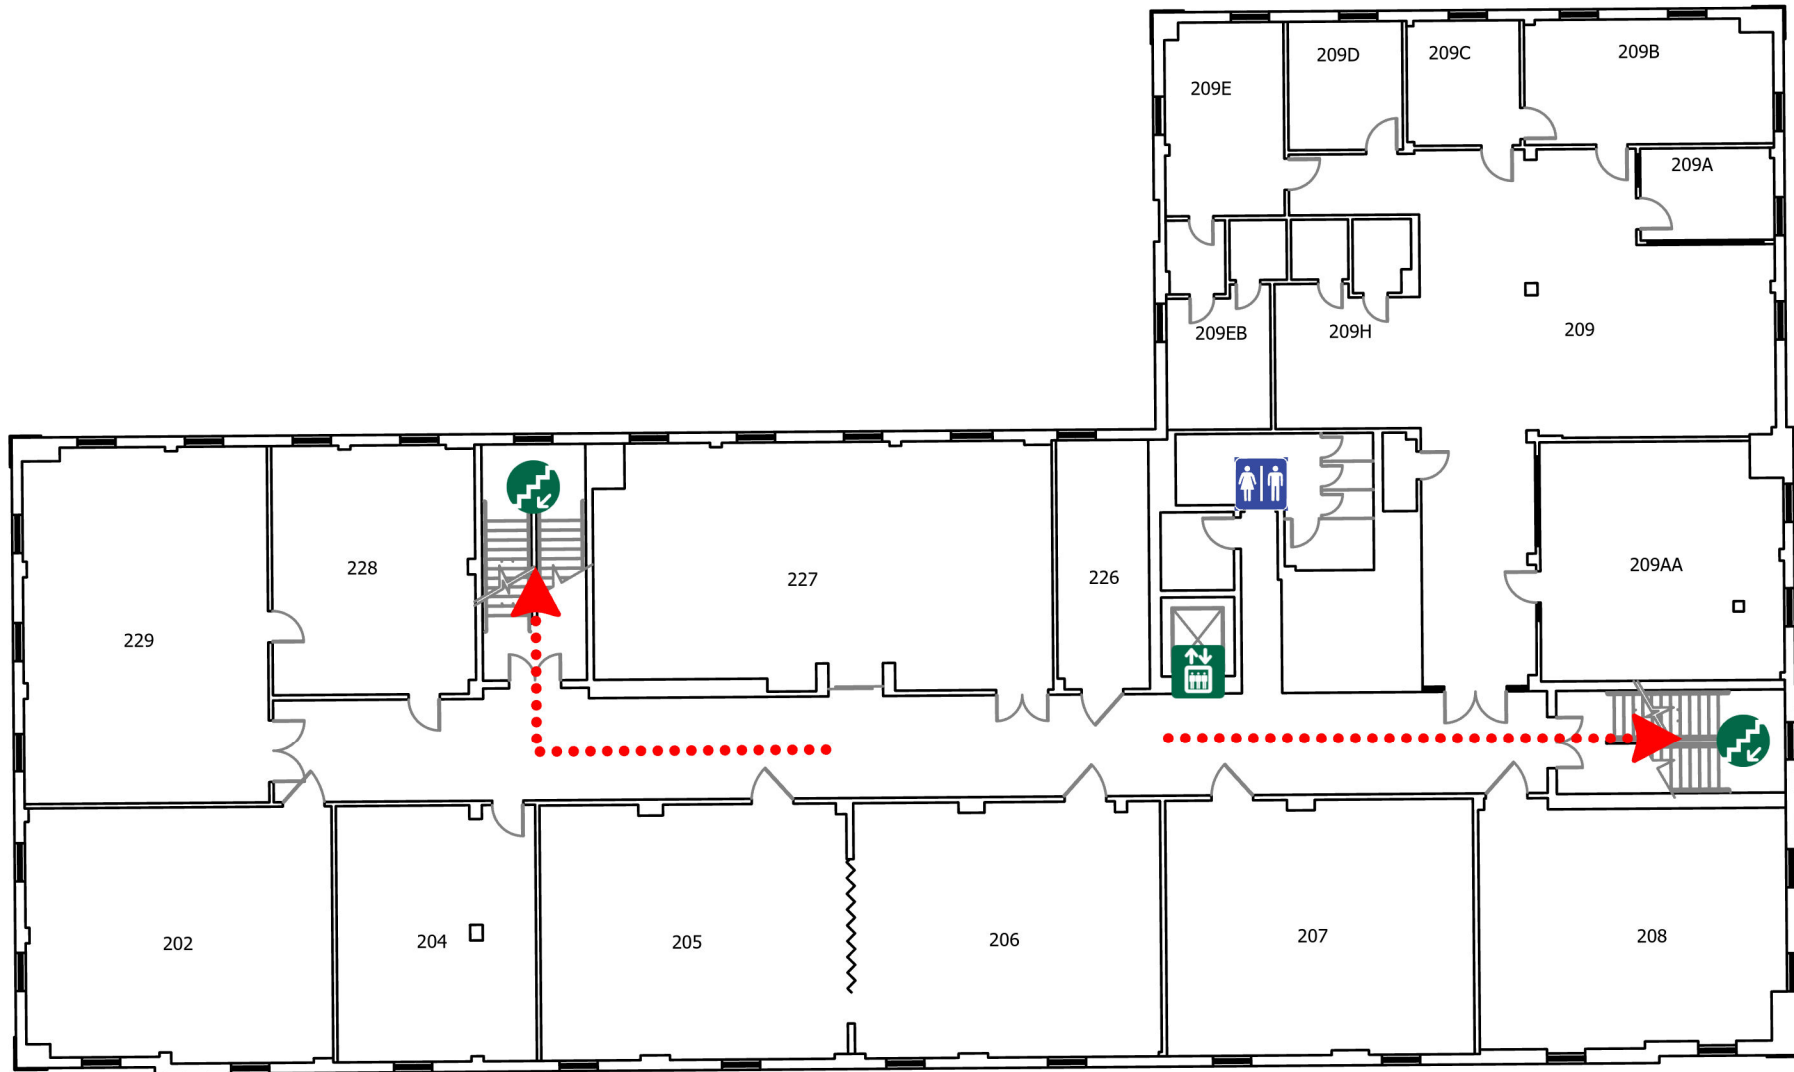

PHYSICS BUILDING

THIRD FLOOR

