


LEGENDS HALL

FIRST FLOOR

N

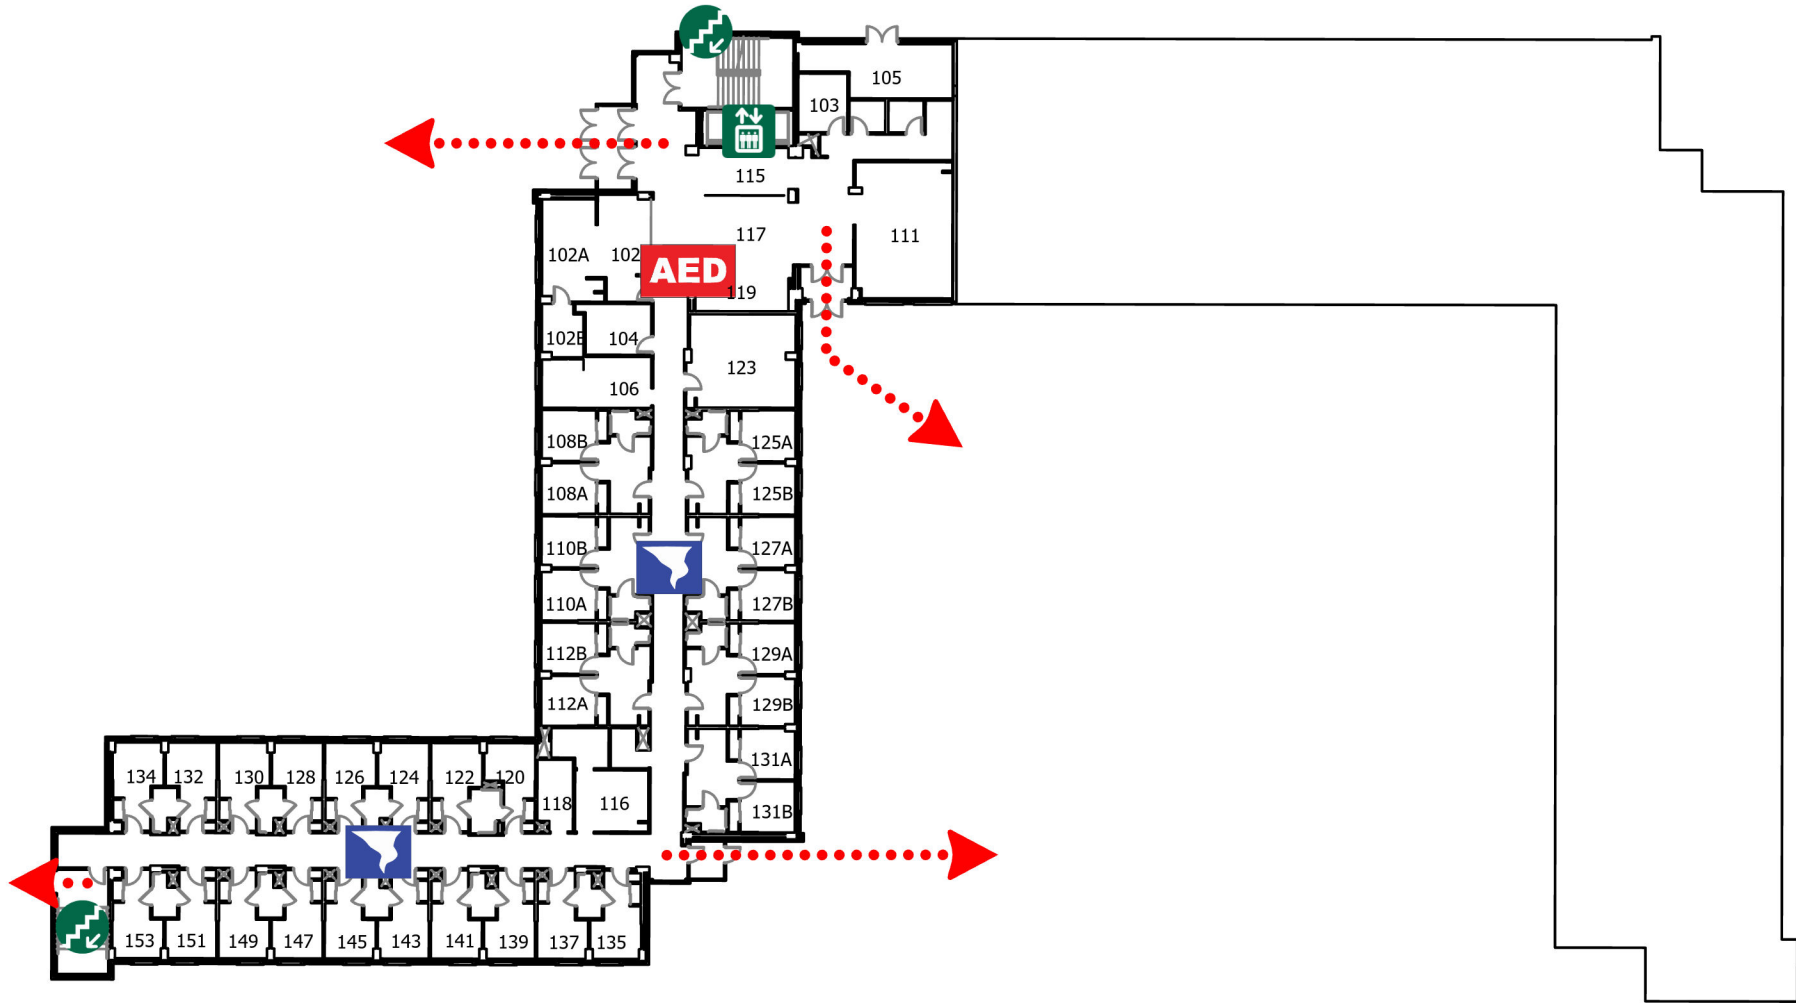

Stairs



Elevator



Shelter Area




AED




Exit

LEGENDS HALL SECOND FLOOR

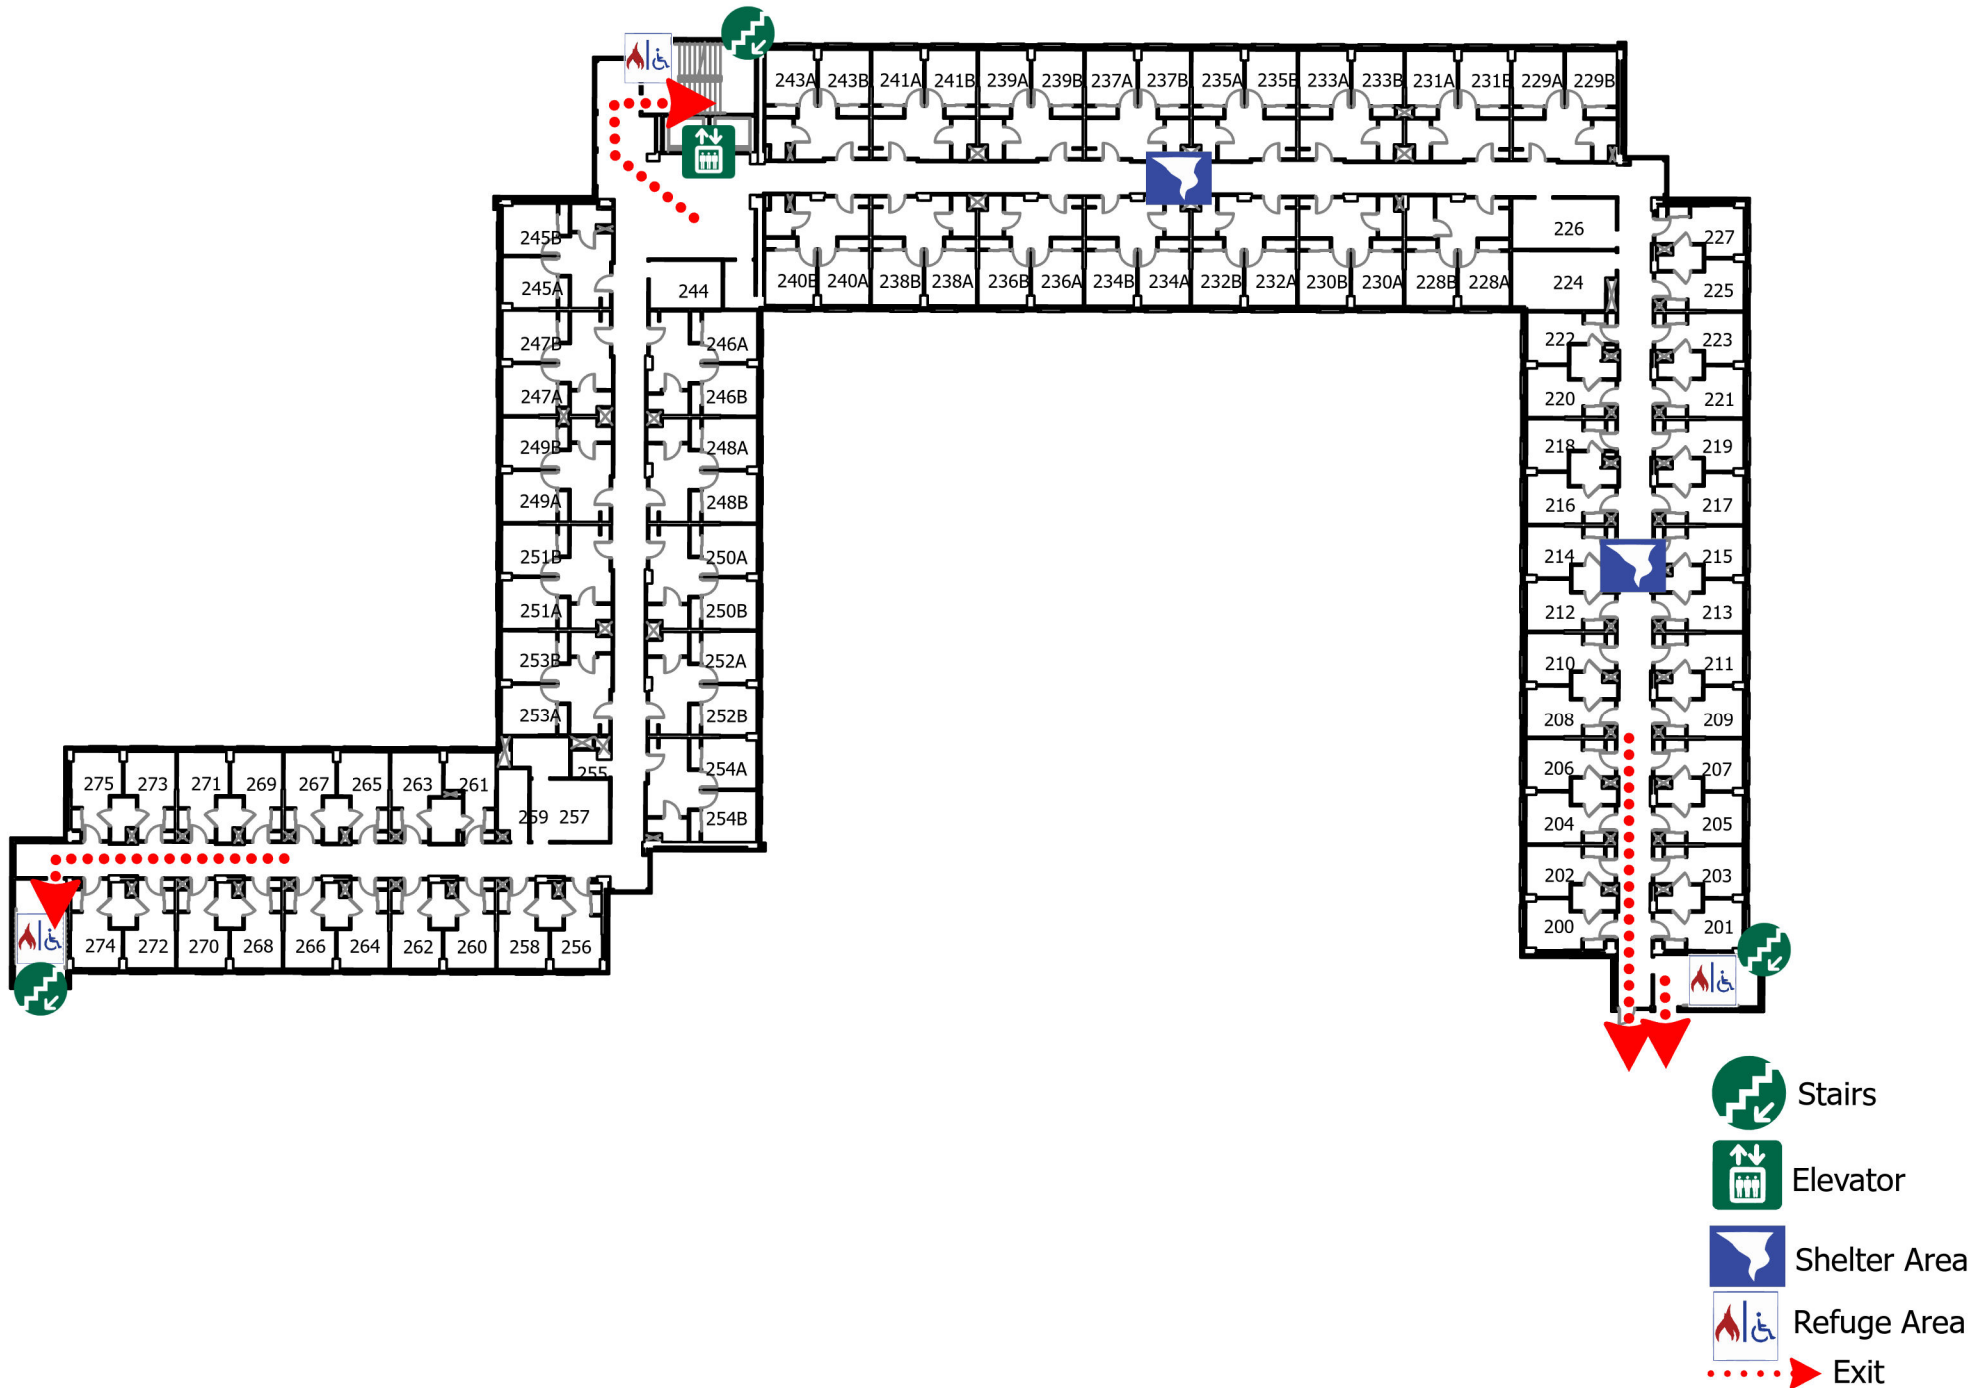

LEGENDS HALL

THIRD FLOOR

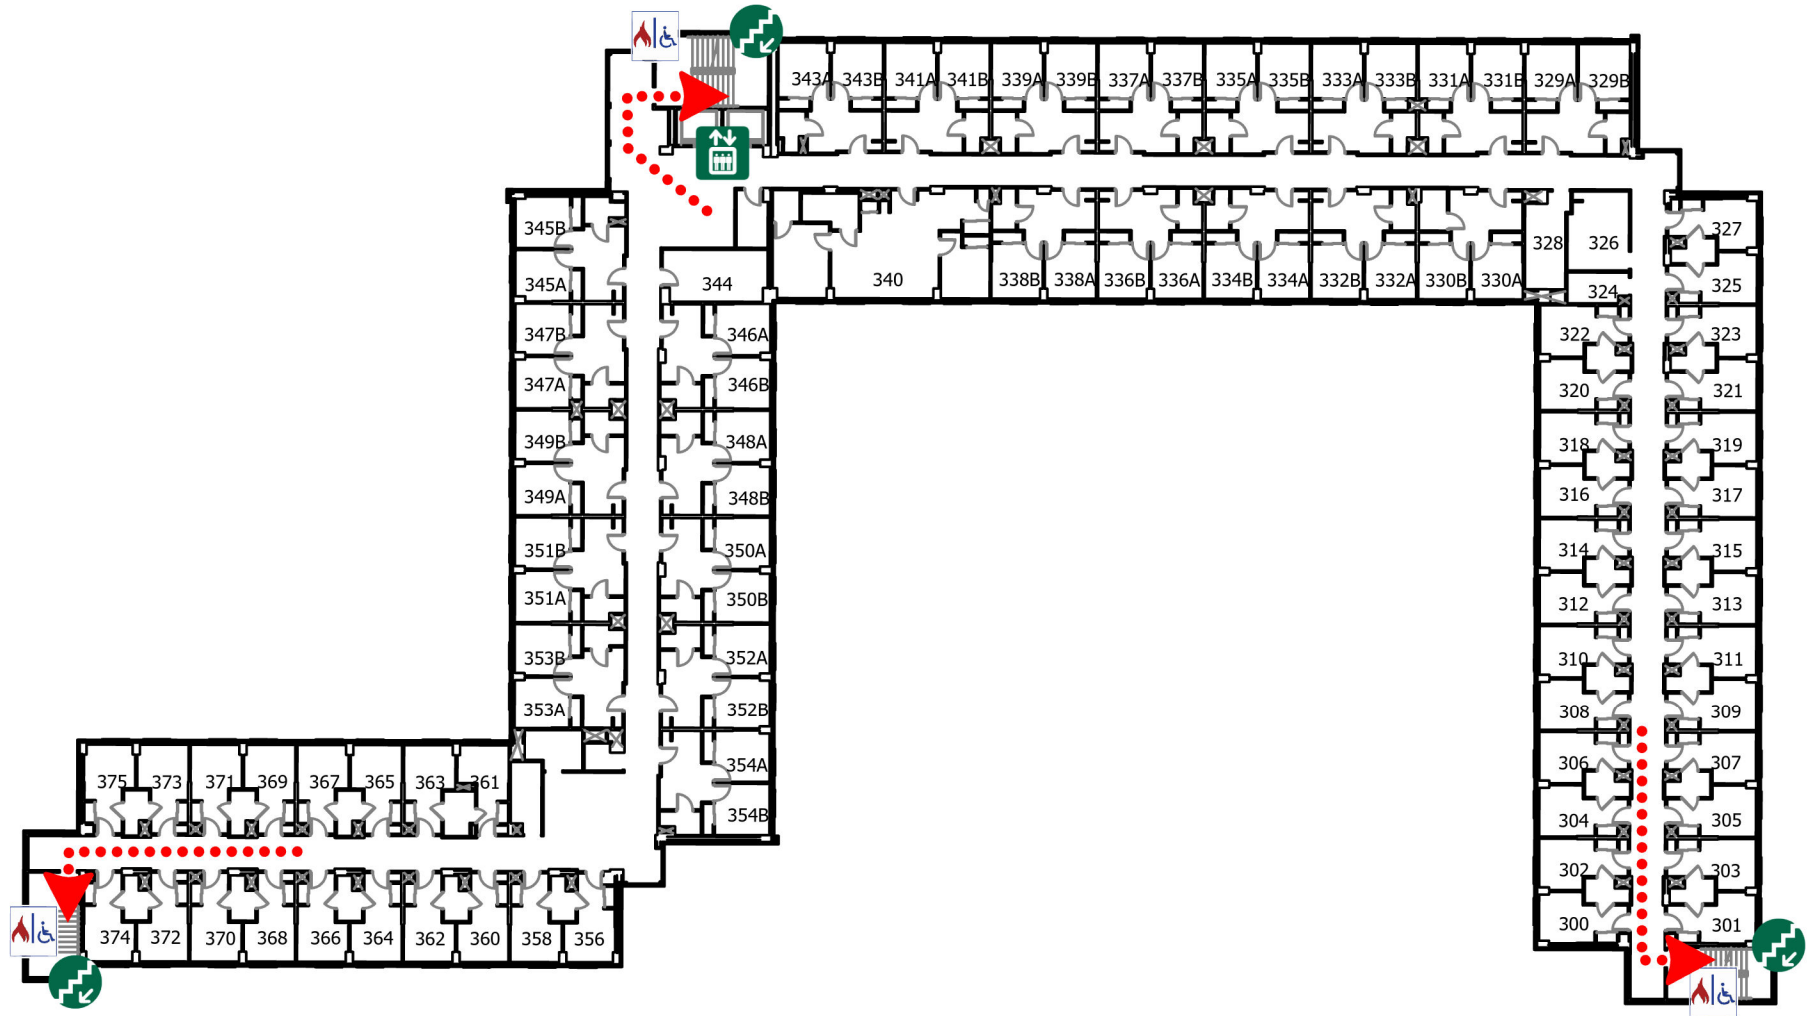

Stairs



Elevator



Refuge Area



Exit

LEGENDS HALL FOURTH FLOOR

