


MUSIC BUILDING

BASEMENT

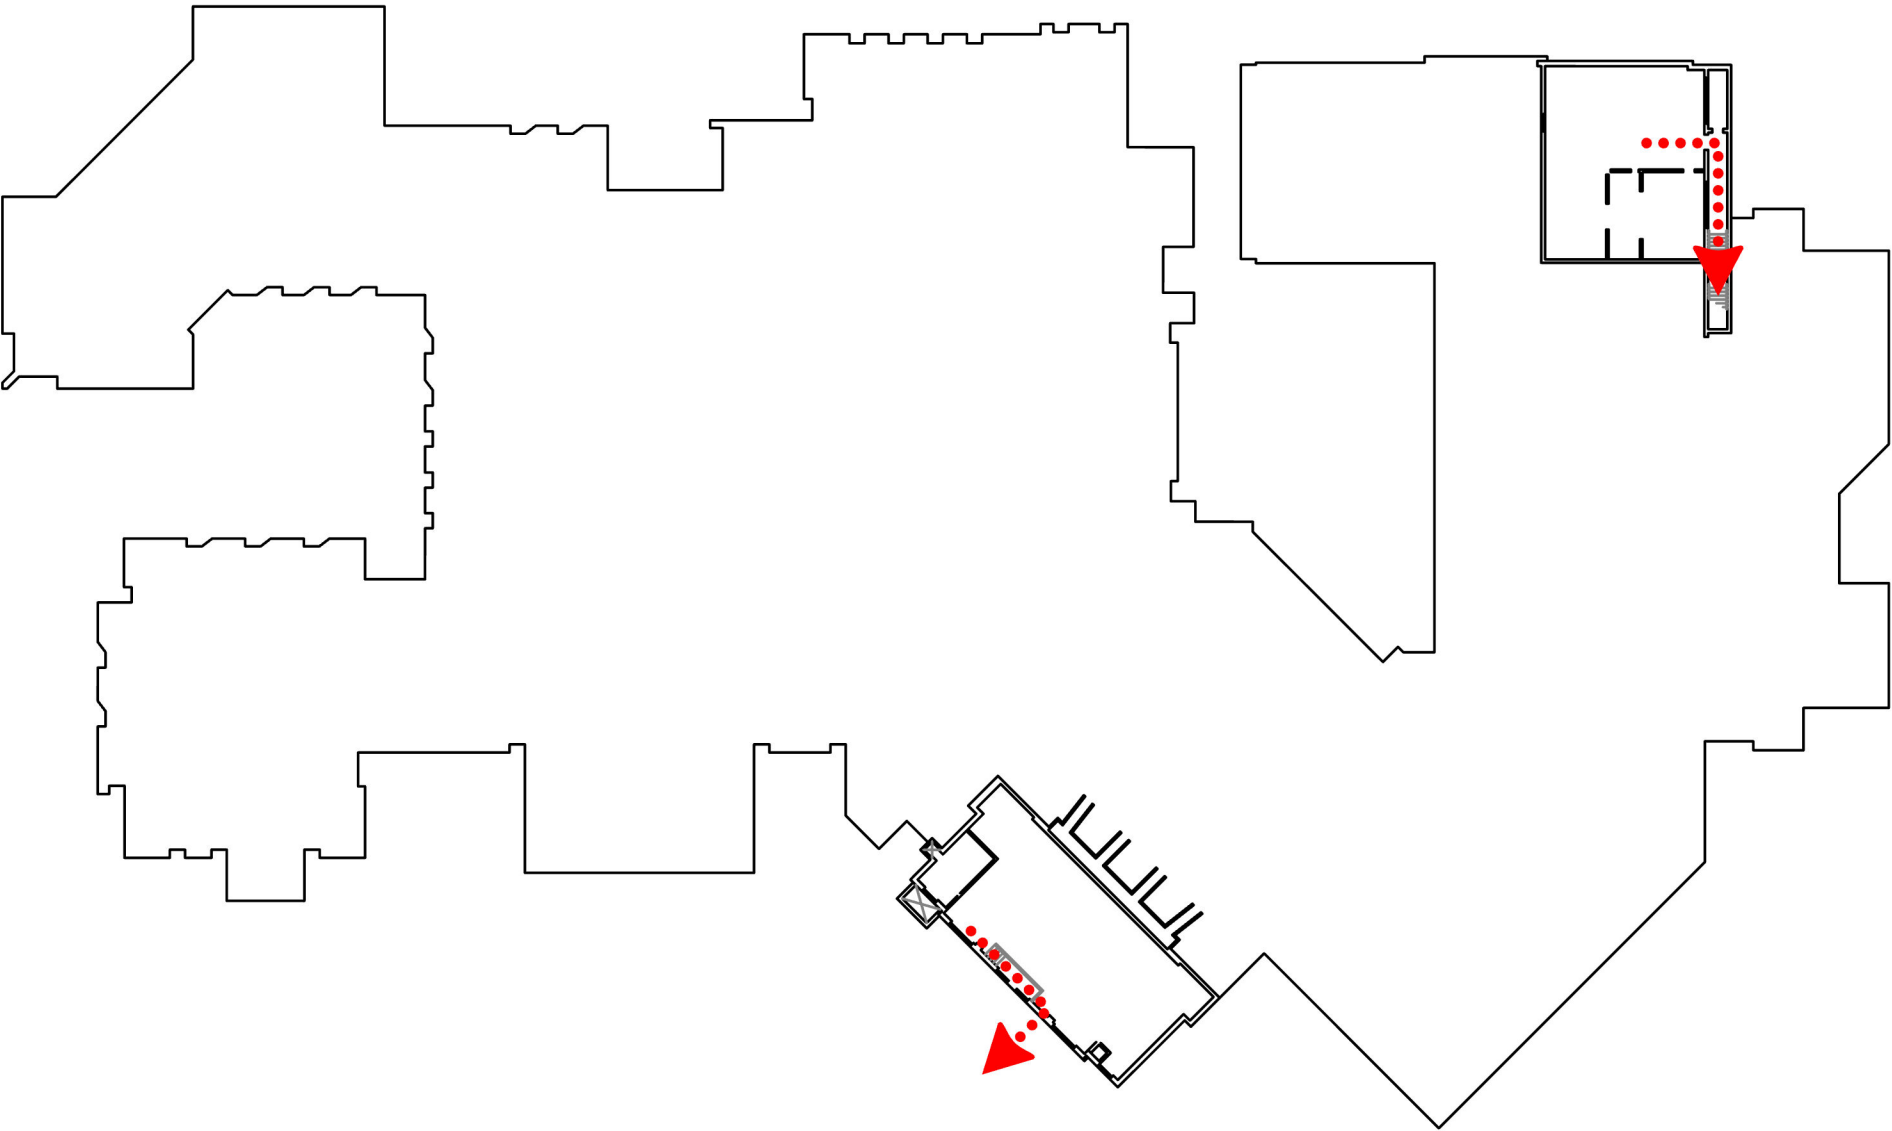

.....▶ Exit

➤ Z




AED AED

Exit


MUSIC BUILDING



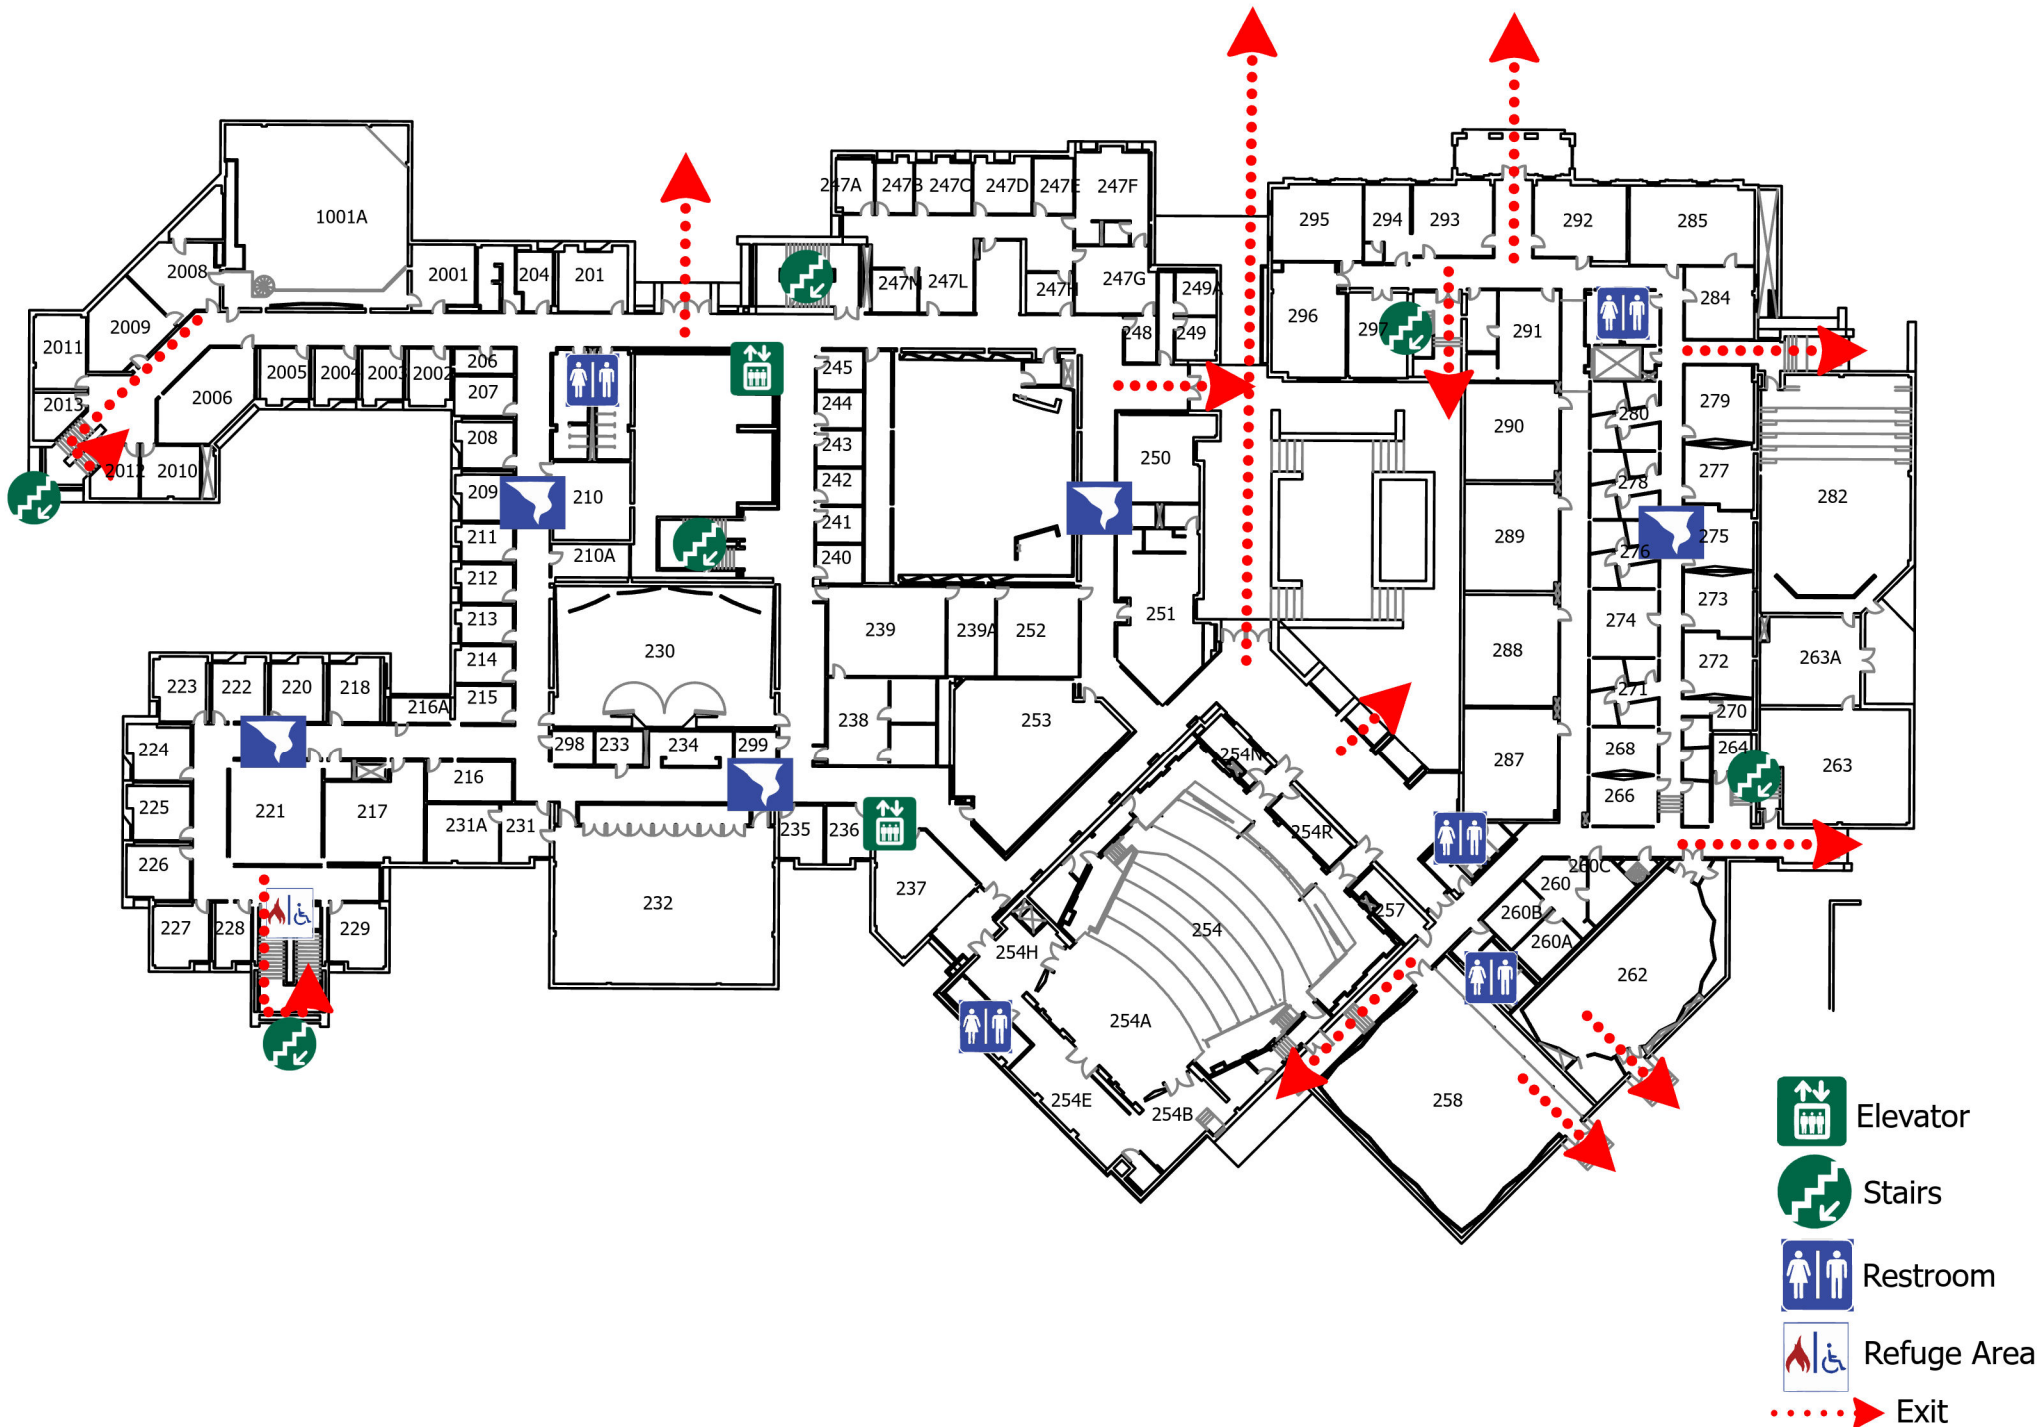

SECOND FLOOR

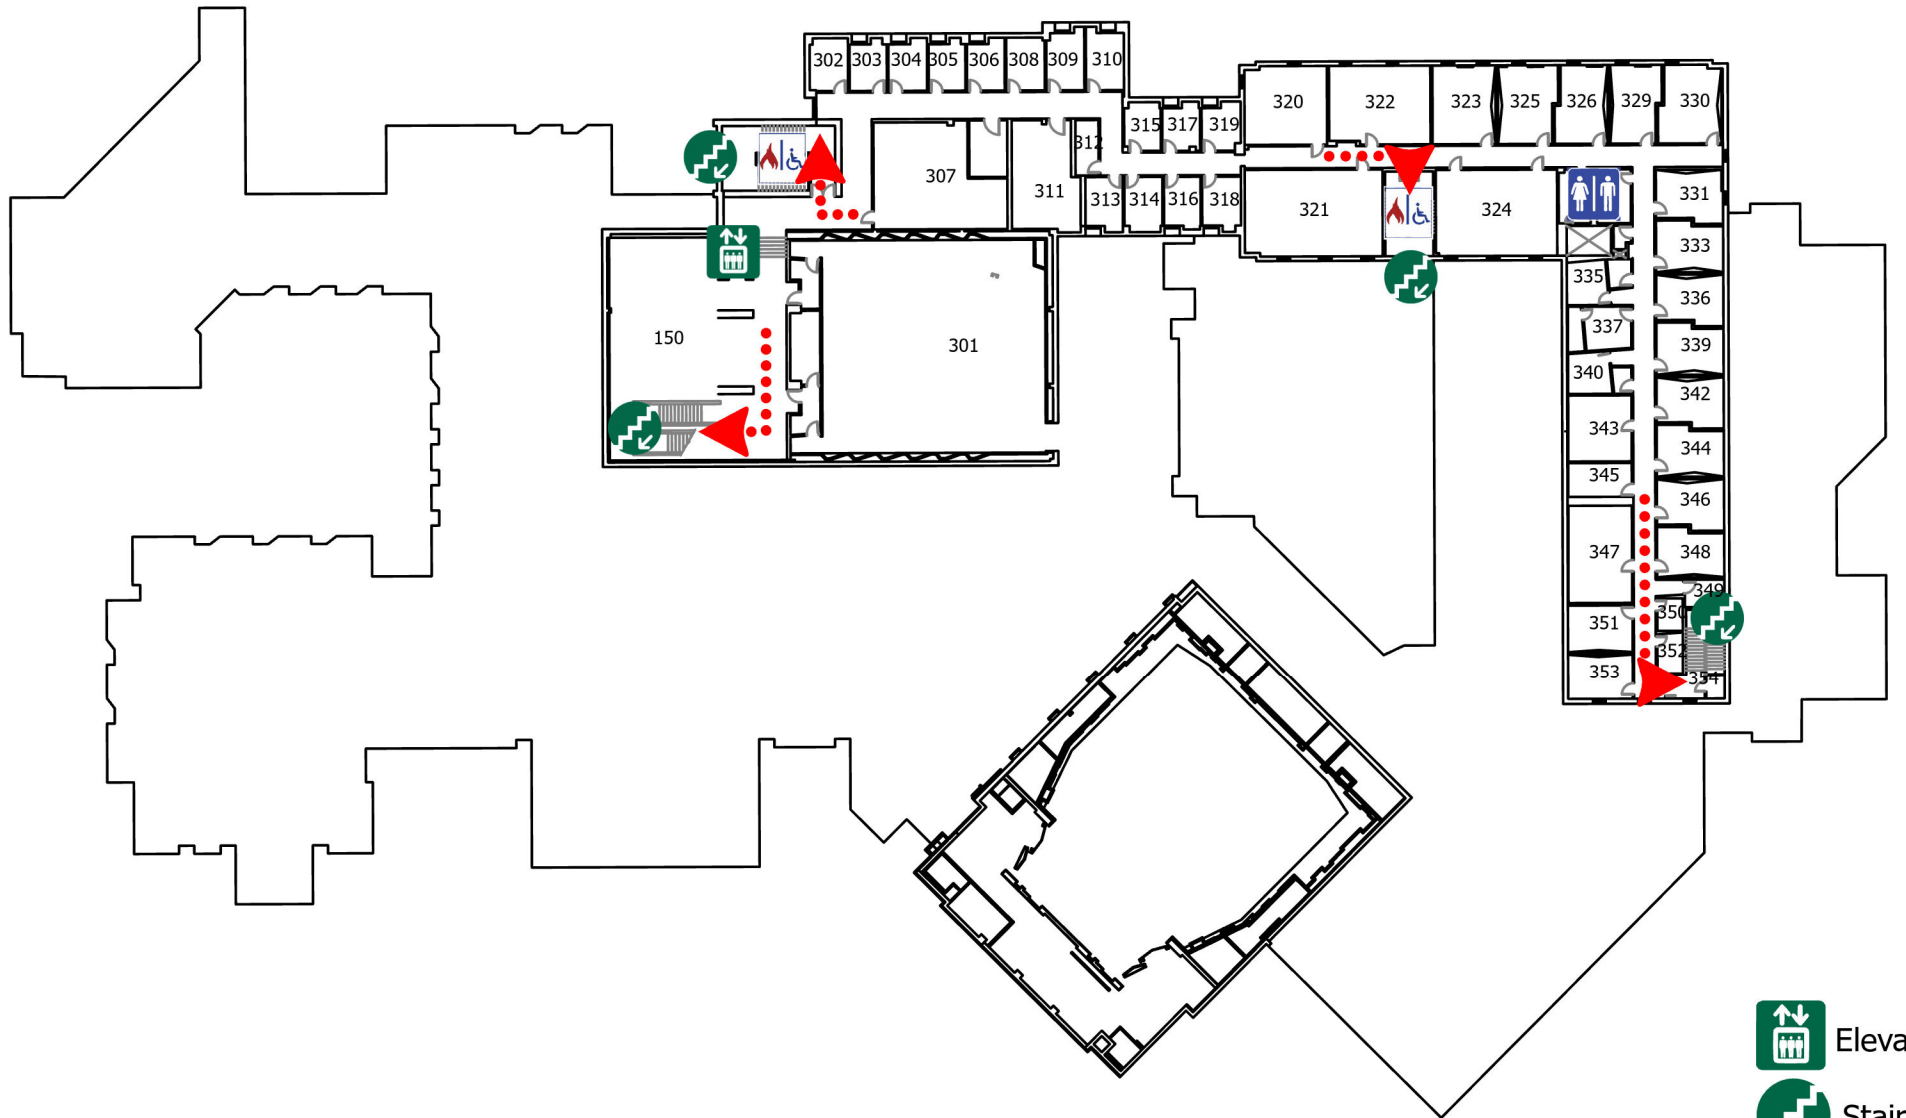

MUSIC BUILDING

THIRD FLOOR



-  Elevator
-  Stairs
-  Restroom
-  Refuge Area
-  Exit